


2025/10/08現在

電話物理配線図

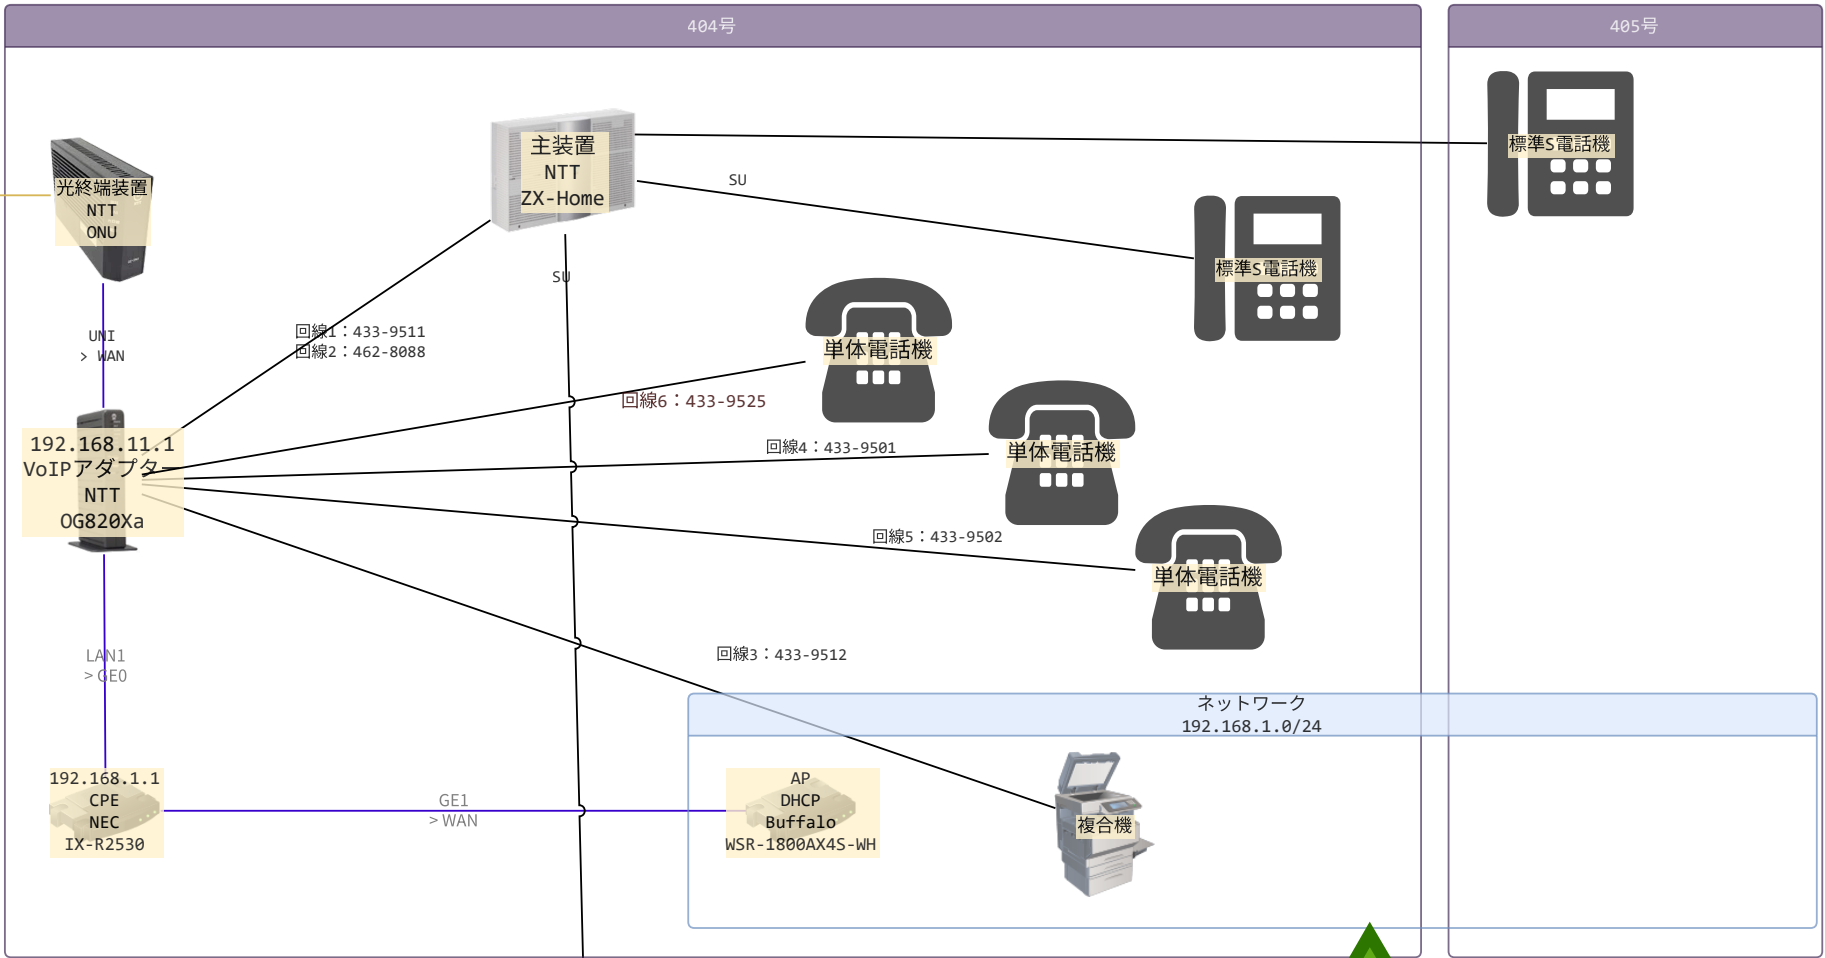


フレッツ光ネクスト
FSHS集



電話物理配線図




フレッツ光ネクスト
FSHS集

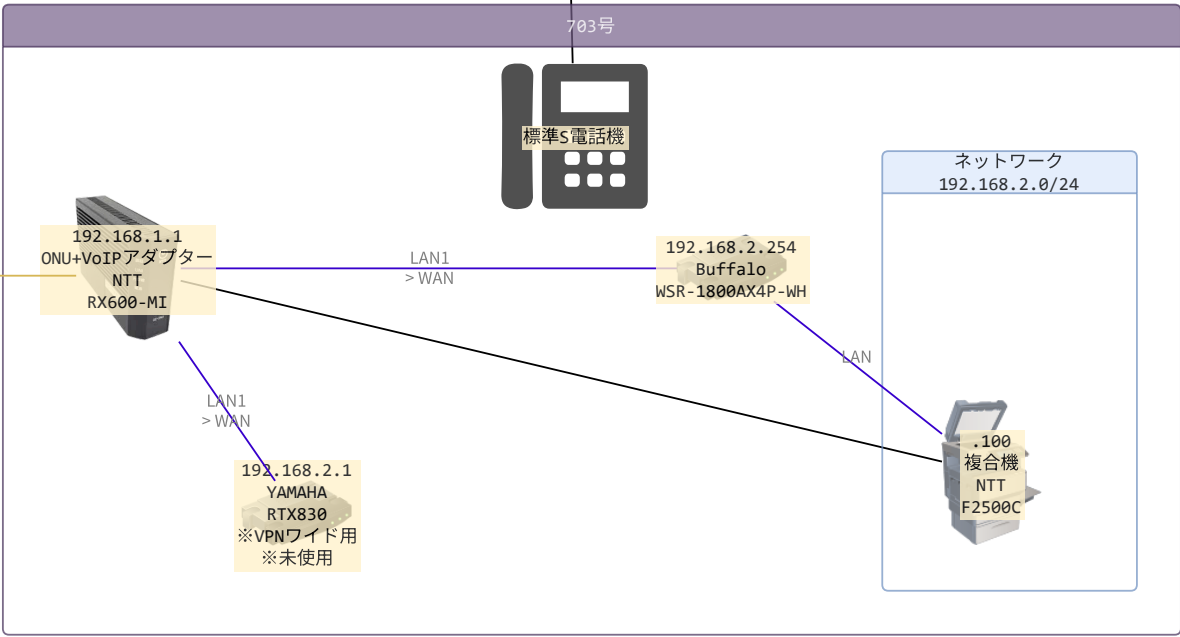

電話物理配線図




フレッツ光ネクスト
FSHS集

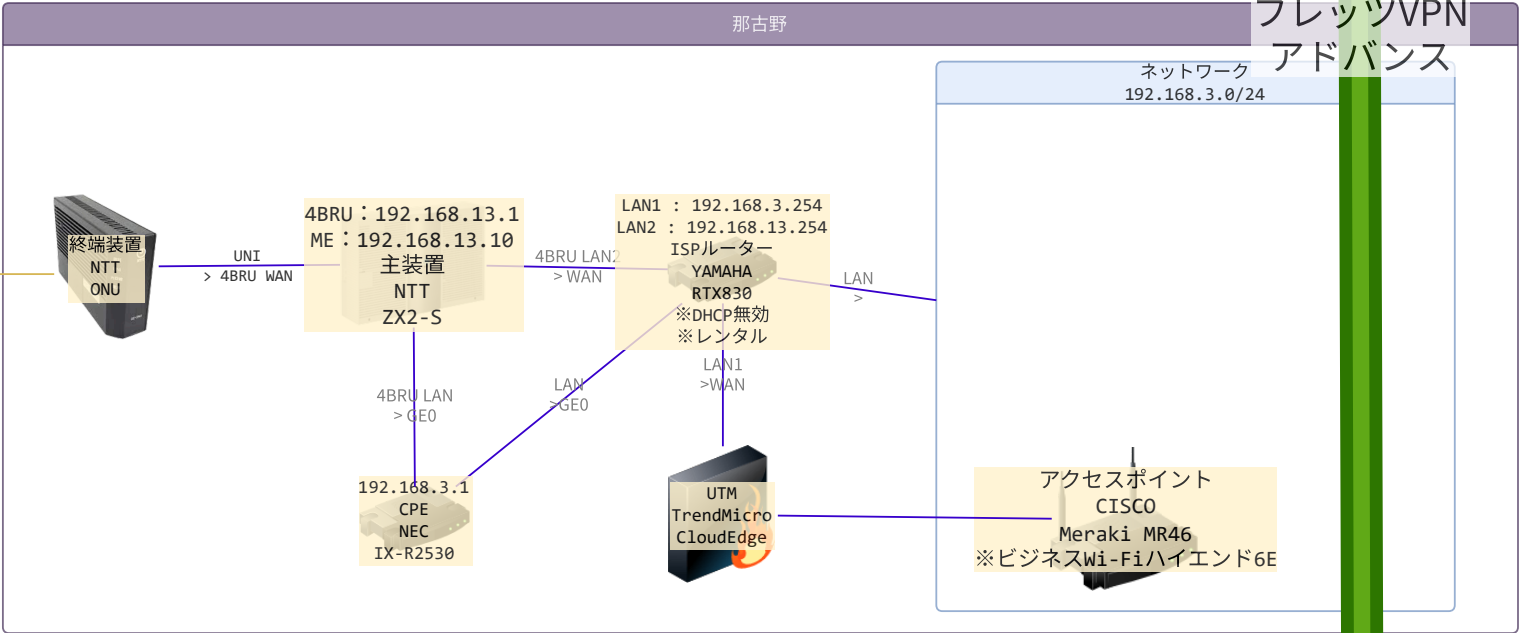


電話物理配線図





フレッツ光ネクスト
FSHS集

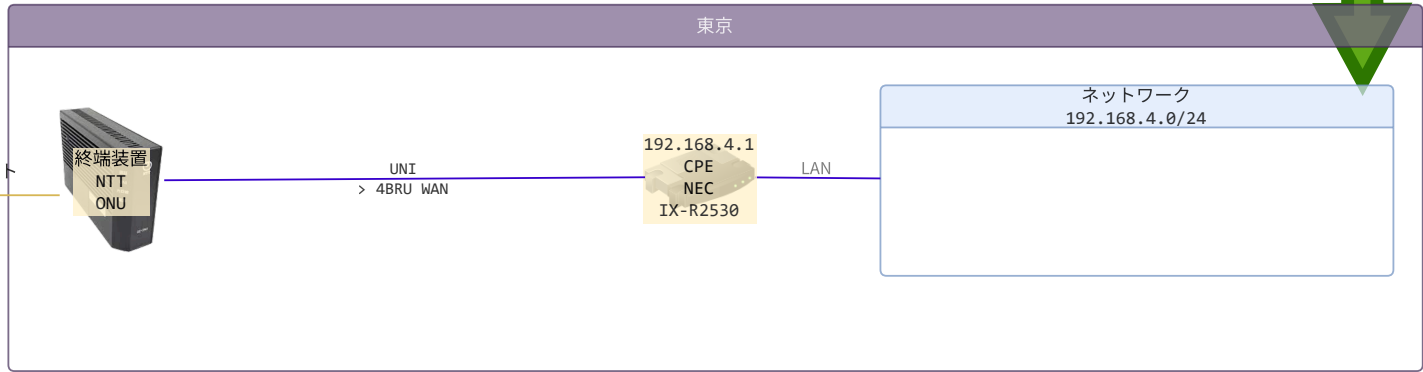


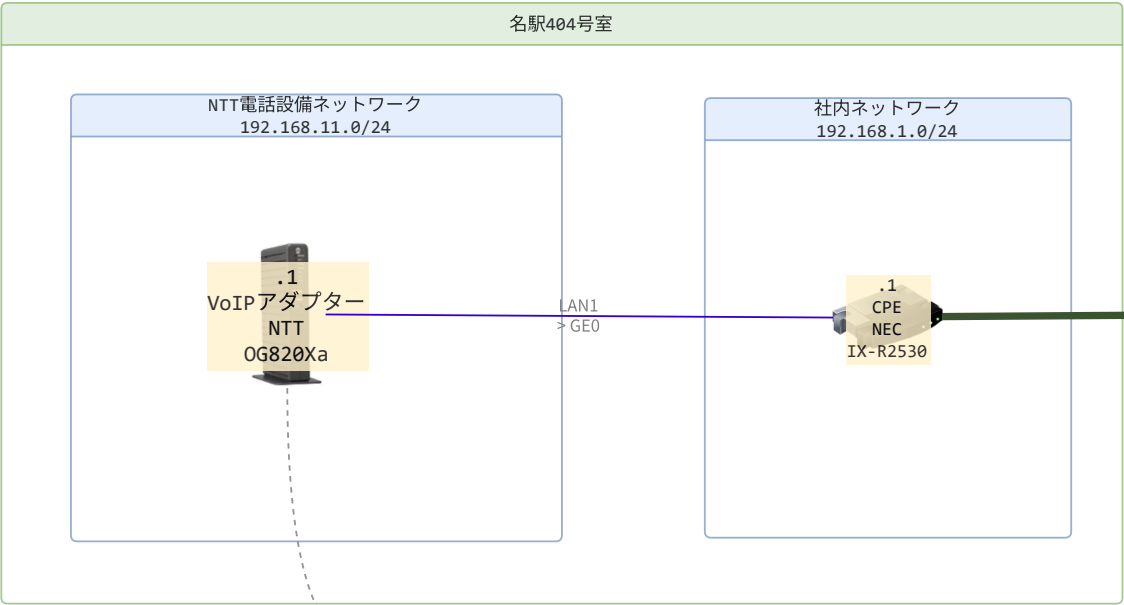

ルーター設置時、OGのアドレスを.1.0/24以外に変更する

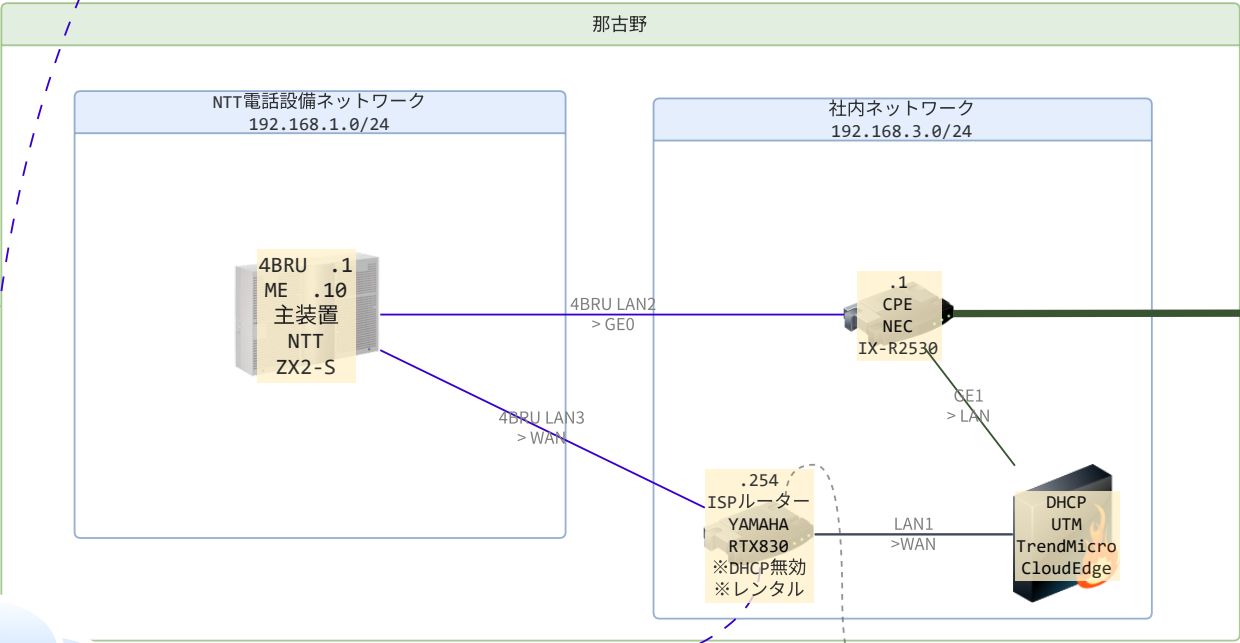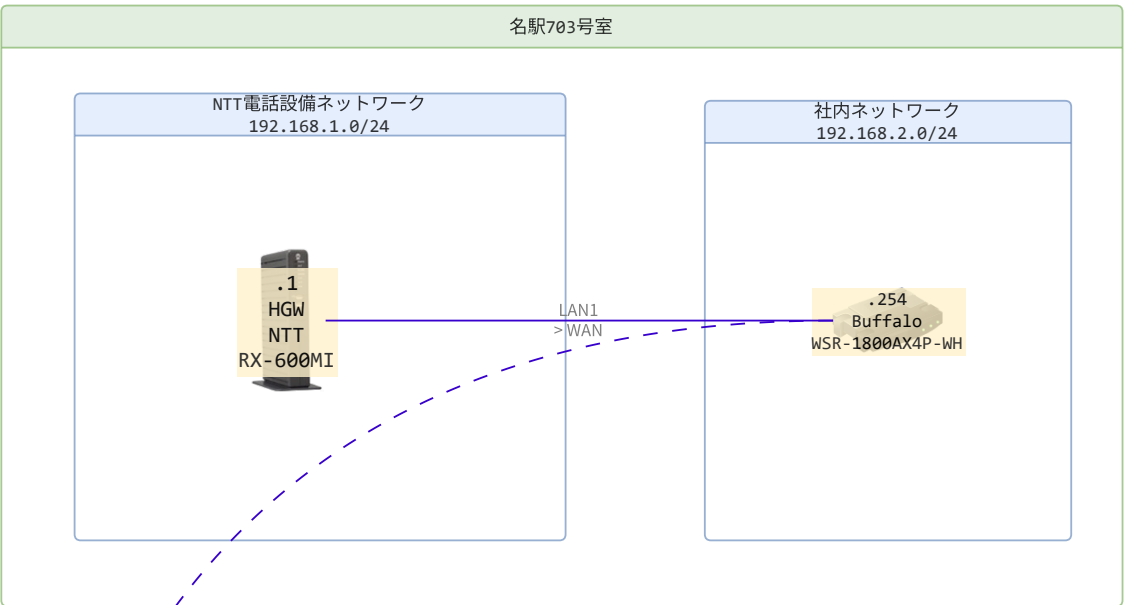

DHCPによるブロードキャストストーム対策
reject LAN2 in udp 67,68

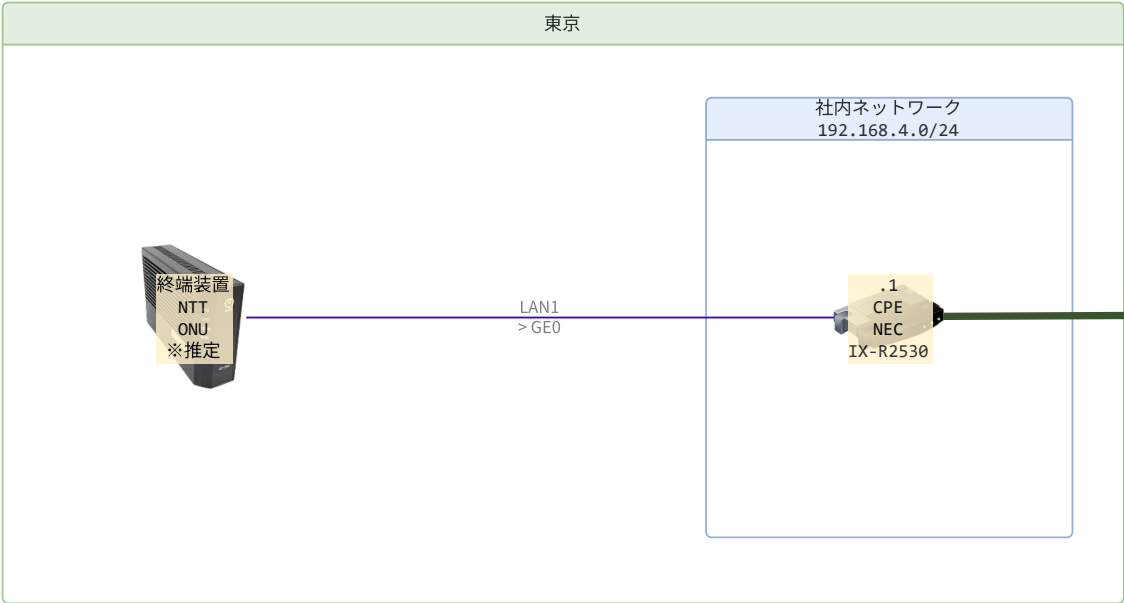


NTT
VPNアドバンス

