



物理配線図

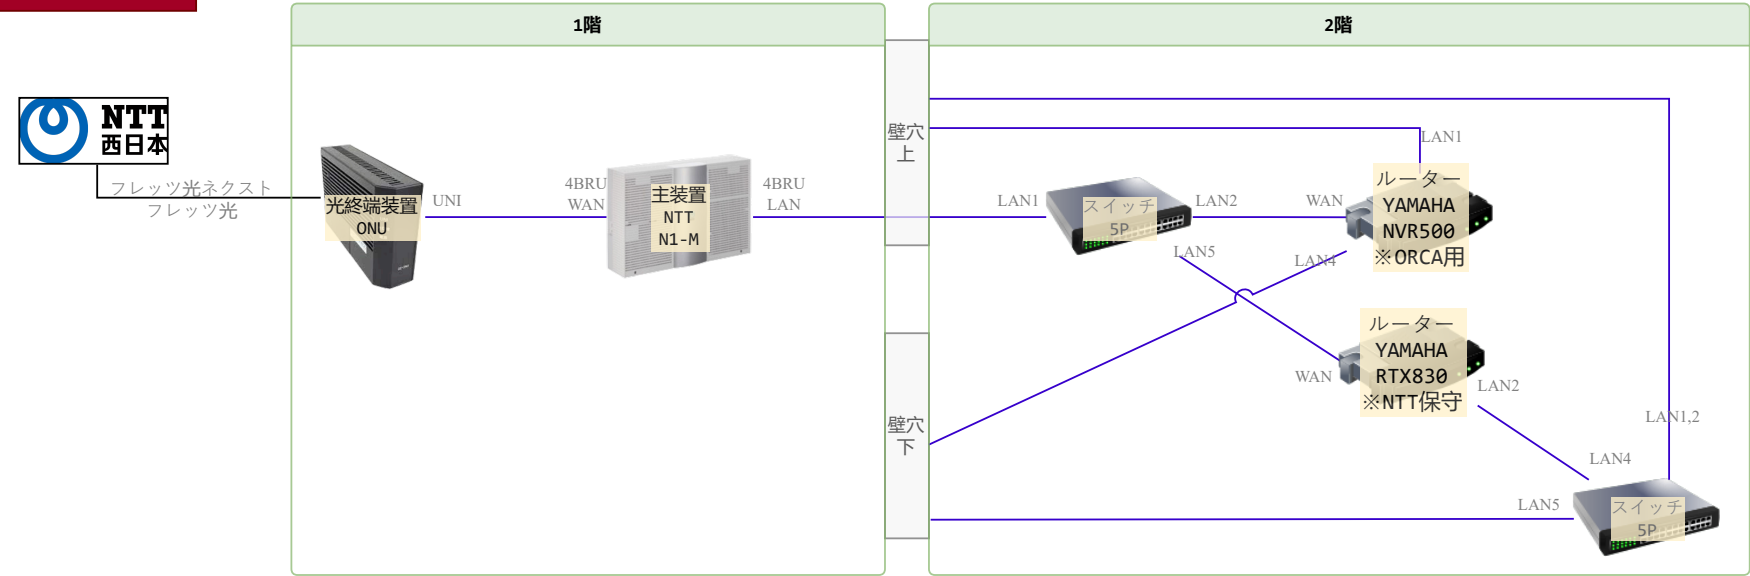


論理構成図

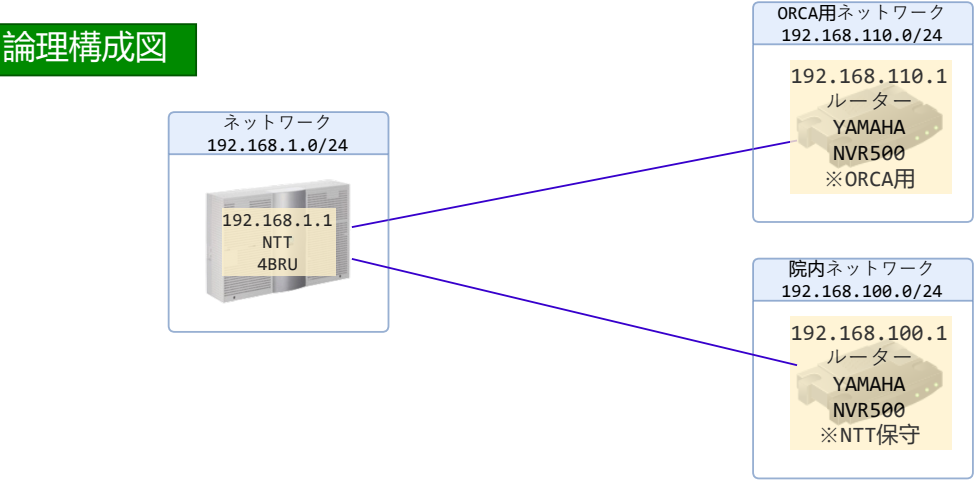

セキュリティおまかせプラン導入イメージ

物理配線図

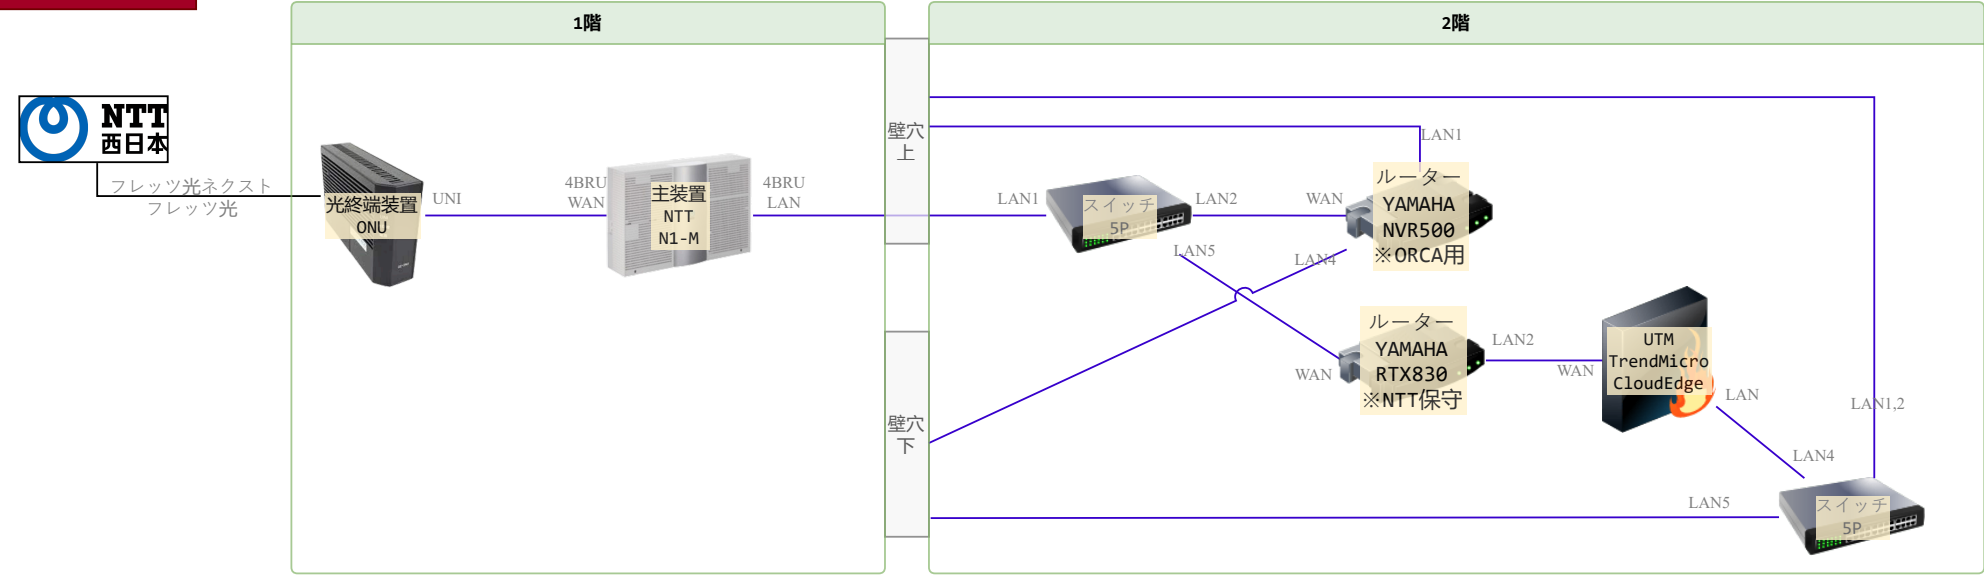

論理構成図

