

名古屋製鋼様 本社改修新築工事

誠実建築


～阿部建設の家～

2024. 2. 1 Version. 2 . 1

ご契約日:

木の香り設計工房

A	0	1	2	3	4	5	6	7	8	9	10	11	12	13	14	15	16	17	18	19			S	1	2	3	4	5	6	7	8	9	10	11			E	1	2			P	1			G	1		
---	---	---	---	---	---	---	---	---	---	---	----	----	----	----	----	----	----	----	----	----	--	--	---	---	---	---	---	---	---	---	---	---	----	----	--	--	---	---	---	--	--	---	---	--	--	---	---	--	--

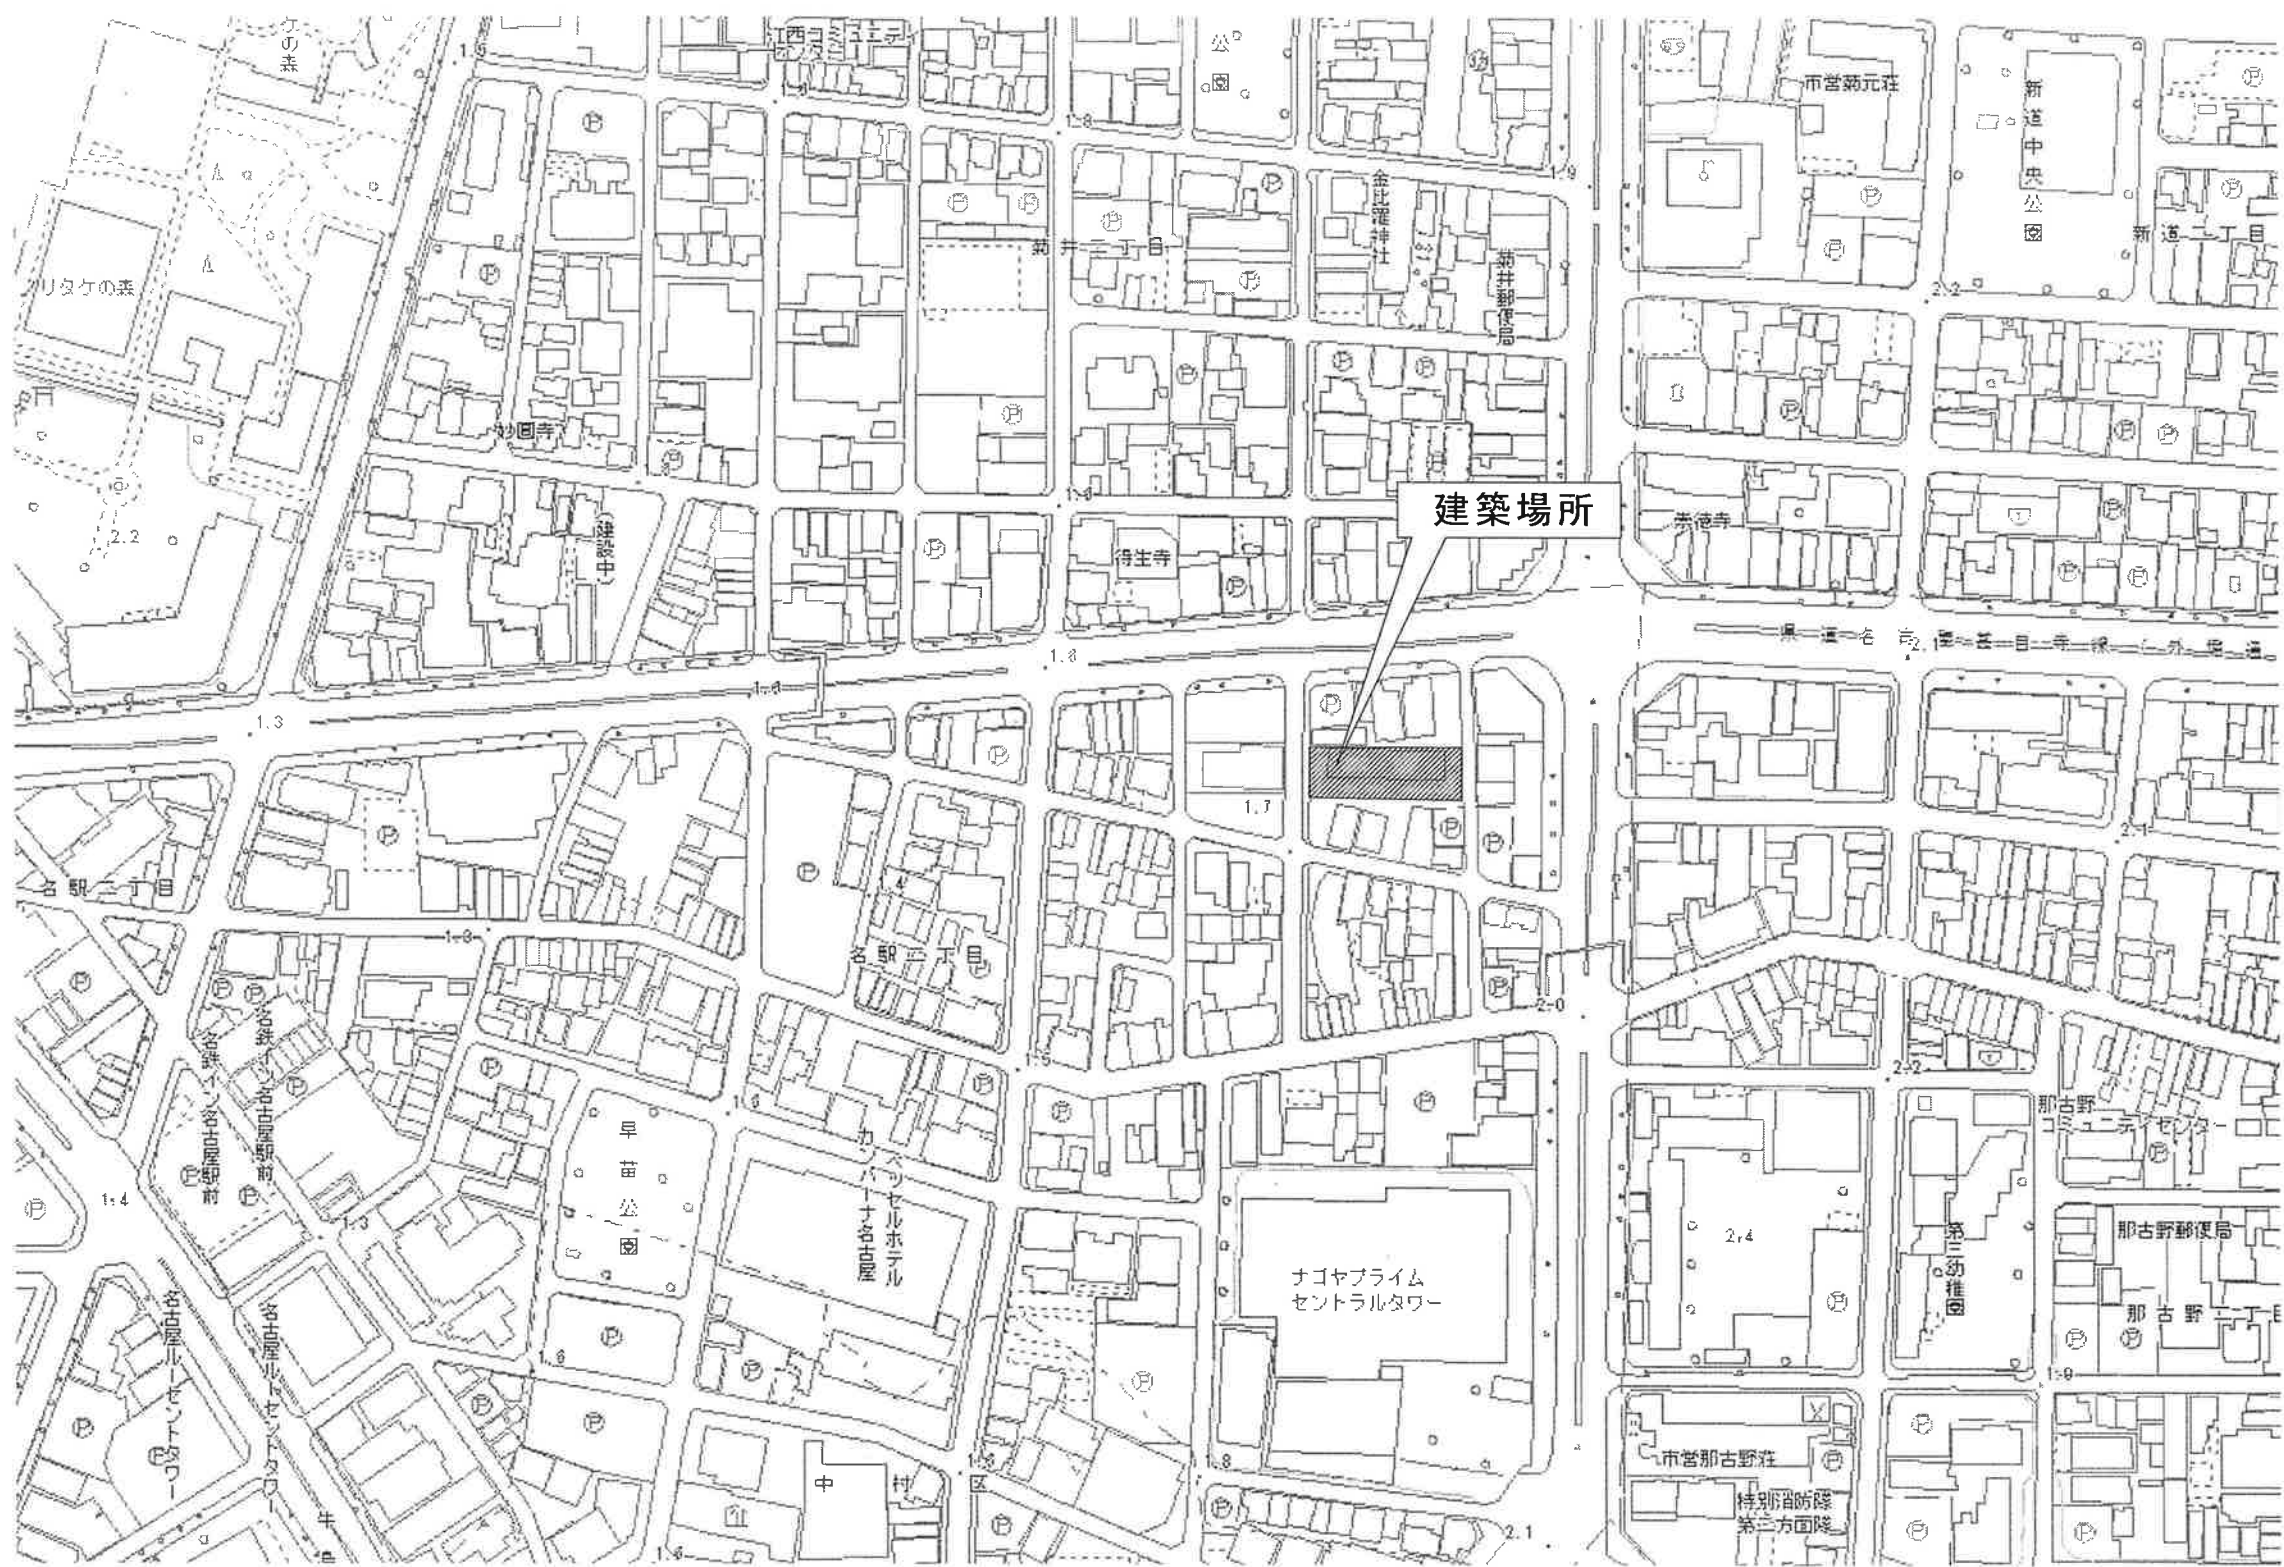


案内図 S = 1 / 2, 500

所在地：名古屋市西区名駅2-4-3

23.06.14

内部仕上表

	床	巾 木	壁	天 井	天井廻縁	備 考
共通事項 1 階	(下地)万協フロア 事務所のみフリーアクセスフロア 断熱材 スタイロフォーム厚15 空気式床暖房		(下地)P.B厚12.5 断熱材 モコフォーム厚100 ※事務所カウンター下は無し	(下地)P.B厚12.5 (大会議室) (下地)P.B厚12.5 (その他クロス下地)		
エントランス	長尺塩ビシート (東リ/FS4040)	長尺シート貼り上げ	ビニルクロス(準不燃) (サンゲツ/TH32029) 一部桧小幅板張り厚10以上 (H12建告1439号)	ジブトーン(不燃)	F見切	カウンター(珪積層板)、インターホン、看板 (別途工事)、ノンスリップ金物 (蓄光ライン入り)
廊下	カーペットタイル (東リ/GA36502)	木製巾木H=60	ビニルクロス(準不燃) (サンゲツ/TH32029)	△	△	
応接室	△	△	ビニルクロス(準不燃) (サンゲツ/TH32029) 一部桧小幅板張り厚10以上 (H12建告1439号)	△	△	固定棚(珪積層板)、机(メラミン化粧板張り)、神棚(別途工事)
倉庫1	△	△	ビニルクロス(準不燃) (サンゲツ/TH32029)	△	△	固定棚(珪積層板)、可動棚
大会議室	△	△	ビニルクロス(不燃) (サンゲツ/TH32029) 一部タイル貼り (LIXIL/サンティエ ECP630/STE1A, ECP303/STE1B, ECP315/STE1B)	△	△	商品展示スペース(珪積層板)、ロールスクリーン用カーテンボックス 新規段差部分:ノンスリップ金物 (蓄光ライン入り)
倉庫2	△	△	ビニルクロス(準不燃) (サンゲツ/TH32029)	△	△	可動棚
倉庫3	△	△	△	△	△	
事務所	△	△	△	△	△	カウンター(珪積層板)、棚 (シナフラッシュ)
バックヤード1	長尺塩ビシート (東リ/FS4040)	ビニル幅木H=60	ビニルクロス(準不燃) (サンゲツ/TH32029)	△	△	ミニキッチン(クリナップ/コラーノ セパレートタイプ W1200,電気温水器3L,レンジフード W450)、 カウンター(メラミン化粧板)、可動棚、ハンガーラック、スロープ
洗面室	△	△	△	△	△	洗面器 (TOTO/MC35)、自動水栓 (TLE26SS2W)、ペーパータオルホルダー (YKT100R) 耐食鏡 (W1200×H1000)、面台 (メラミン化粧板)
WC1	△	△	△	△	△	洋式便器 (TOTO/CS340B+SH340BA)、ウォシュレット (TOTO/TCF6623)、 紙巻器 (TOTO/YH702)、面台 (メラミン化粧板)
WC2	△	△	△	△	△	洋式便器 (TOTO/CS340B+SH340BA)、ウォシュレット (TOTO/TCF6623)、 紙巻器 (TOTO/YH702)、面台 (メラミン化粧板)、ペーパータオルホルダー (YKT100R) 洗面器 (TOTO/LSG722AAPNW)、耐食鏡 (W1000×H1000)、カウンター(メラミン化粧板)
サーバルーム	△	△	△	既存コンクリートスラブアライシ	△	
バックヤード2	既存のまま 一部長尺塩ビシート (東リ/FS4040)	ビニル幅木H=60 一部長尺シート貼り上げ	ビニルクロス(準不燃) (サンゲツ/TH32029) 一部既存RC壁のまま	△	△	新規段差部分:ノンスリップ金物 (蓄光ライン入り) 階段 (既存のまま)
女子更衣室	既存のまま	ビニル幅木H=60	△	既存のまま	△	
男子更衣室	△	△	△	△	△	窓カバー工法 (住宅用・非防火)
地下倉庫	△	—	既存のまま	△	△	窓カバー工法 (住宅用・非防火)

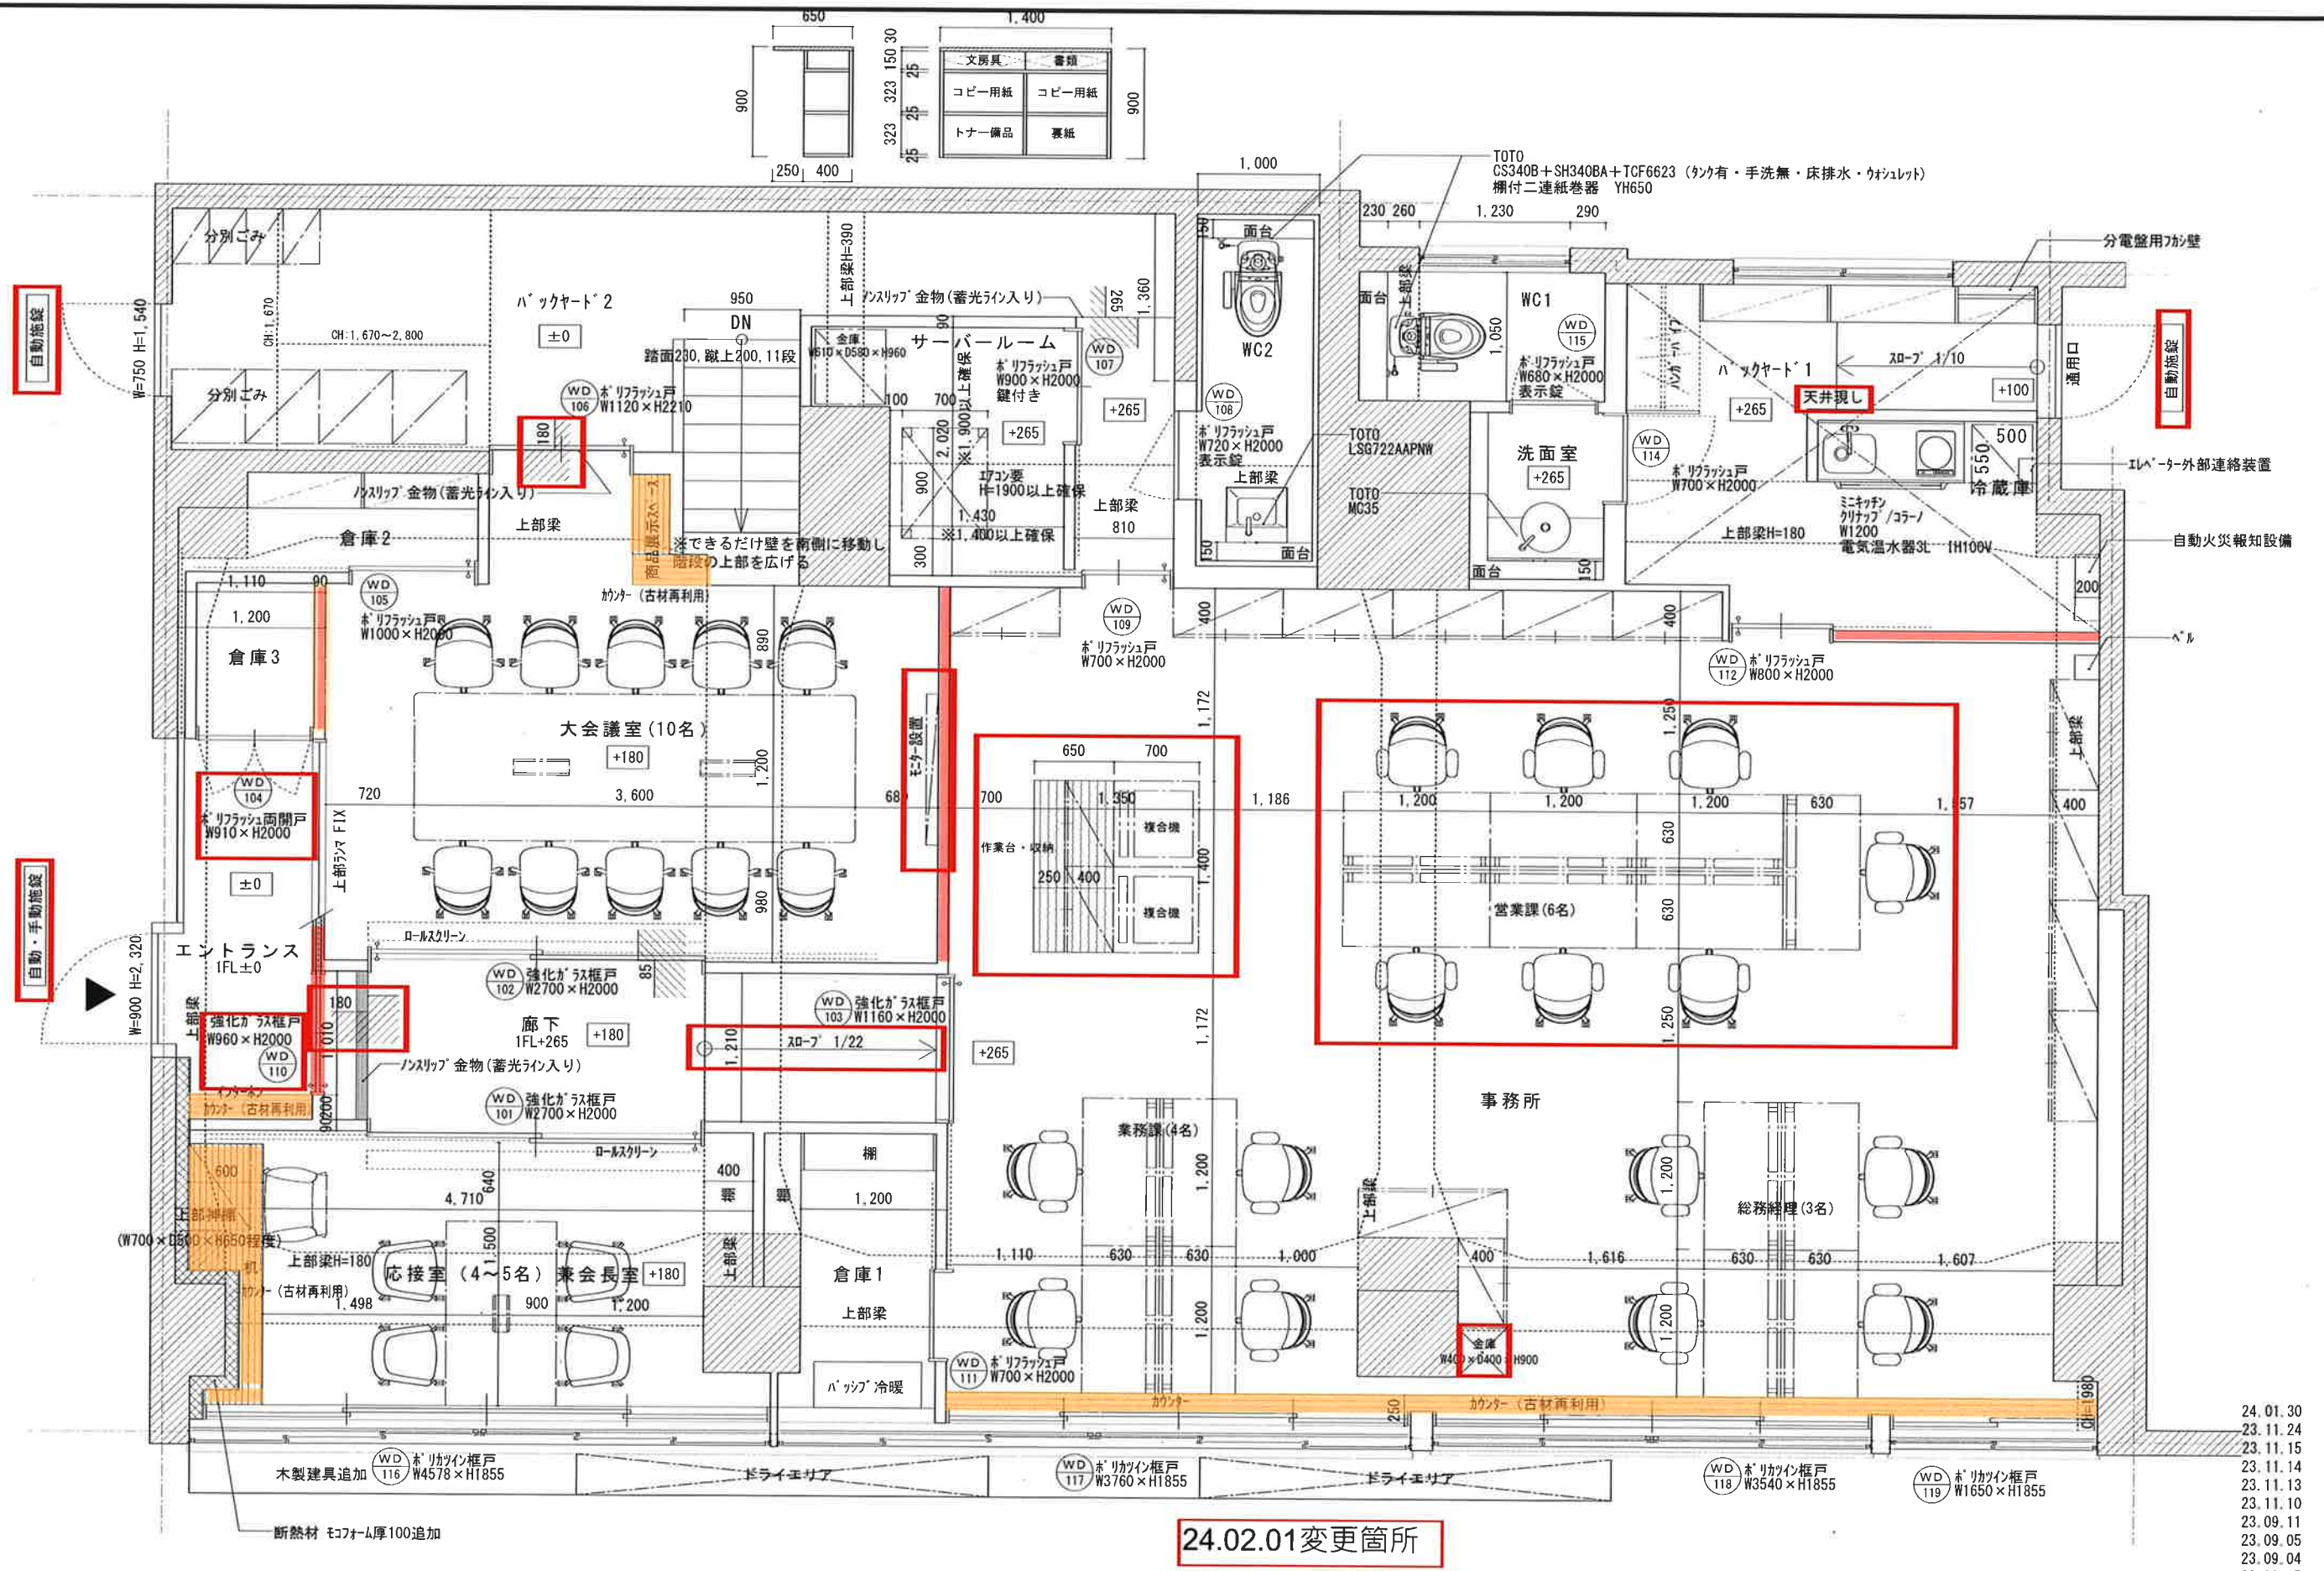

所在地：名古屋市西区名駅2-4-3

誠実建築

～阿部建設の家～

工事名

名古屋製網本社 改修工事

図面名


1階平面図 S=1/50

木の香り設計工房

一級建築士登録第350723号

中村 徹

NO. A-3

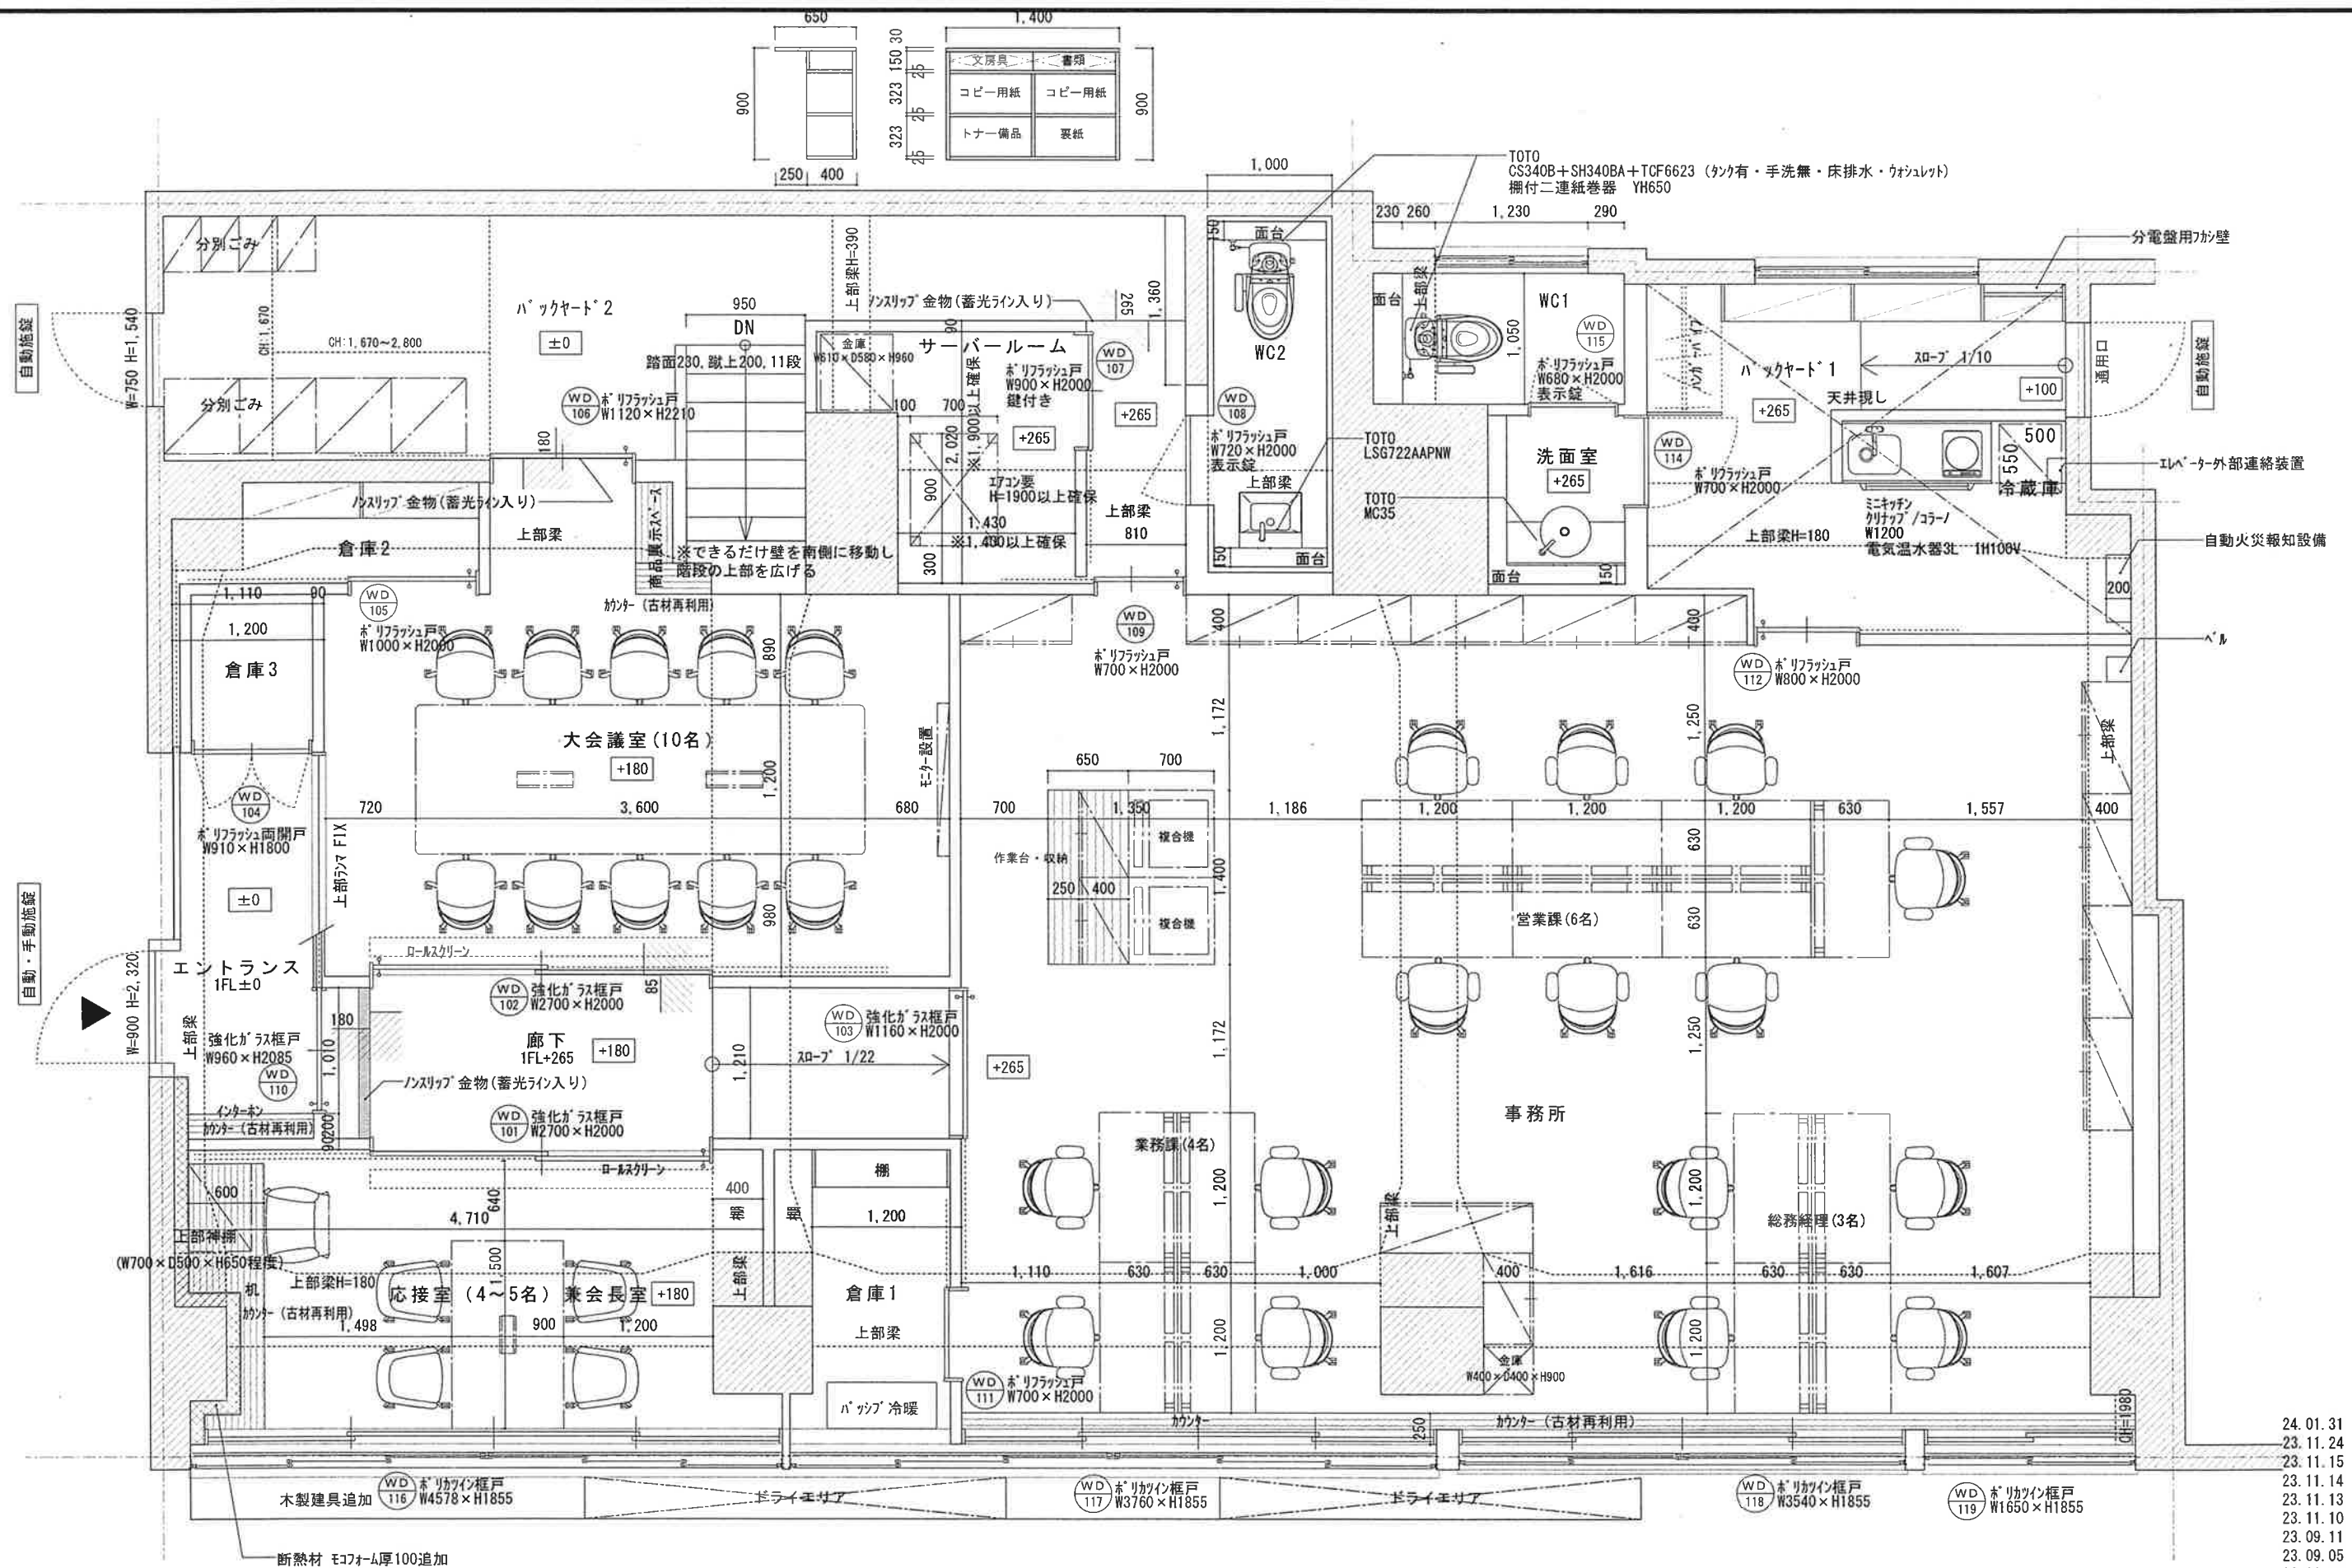

所在地：名古屋市西区名駅2-4-3

誠実建築

～阿部建設の家～

工事名

名古屋製網本社 改修工事


図面名

1階平面図 S=1/50

木の香り設計工房


一級建築士登録第350723号
中村 徹

A-3

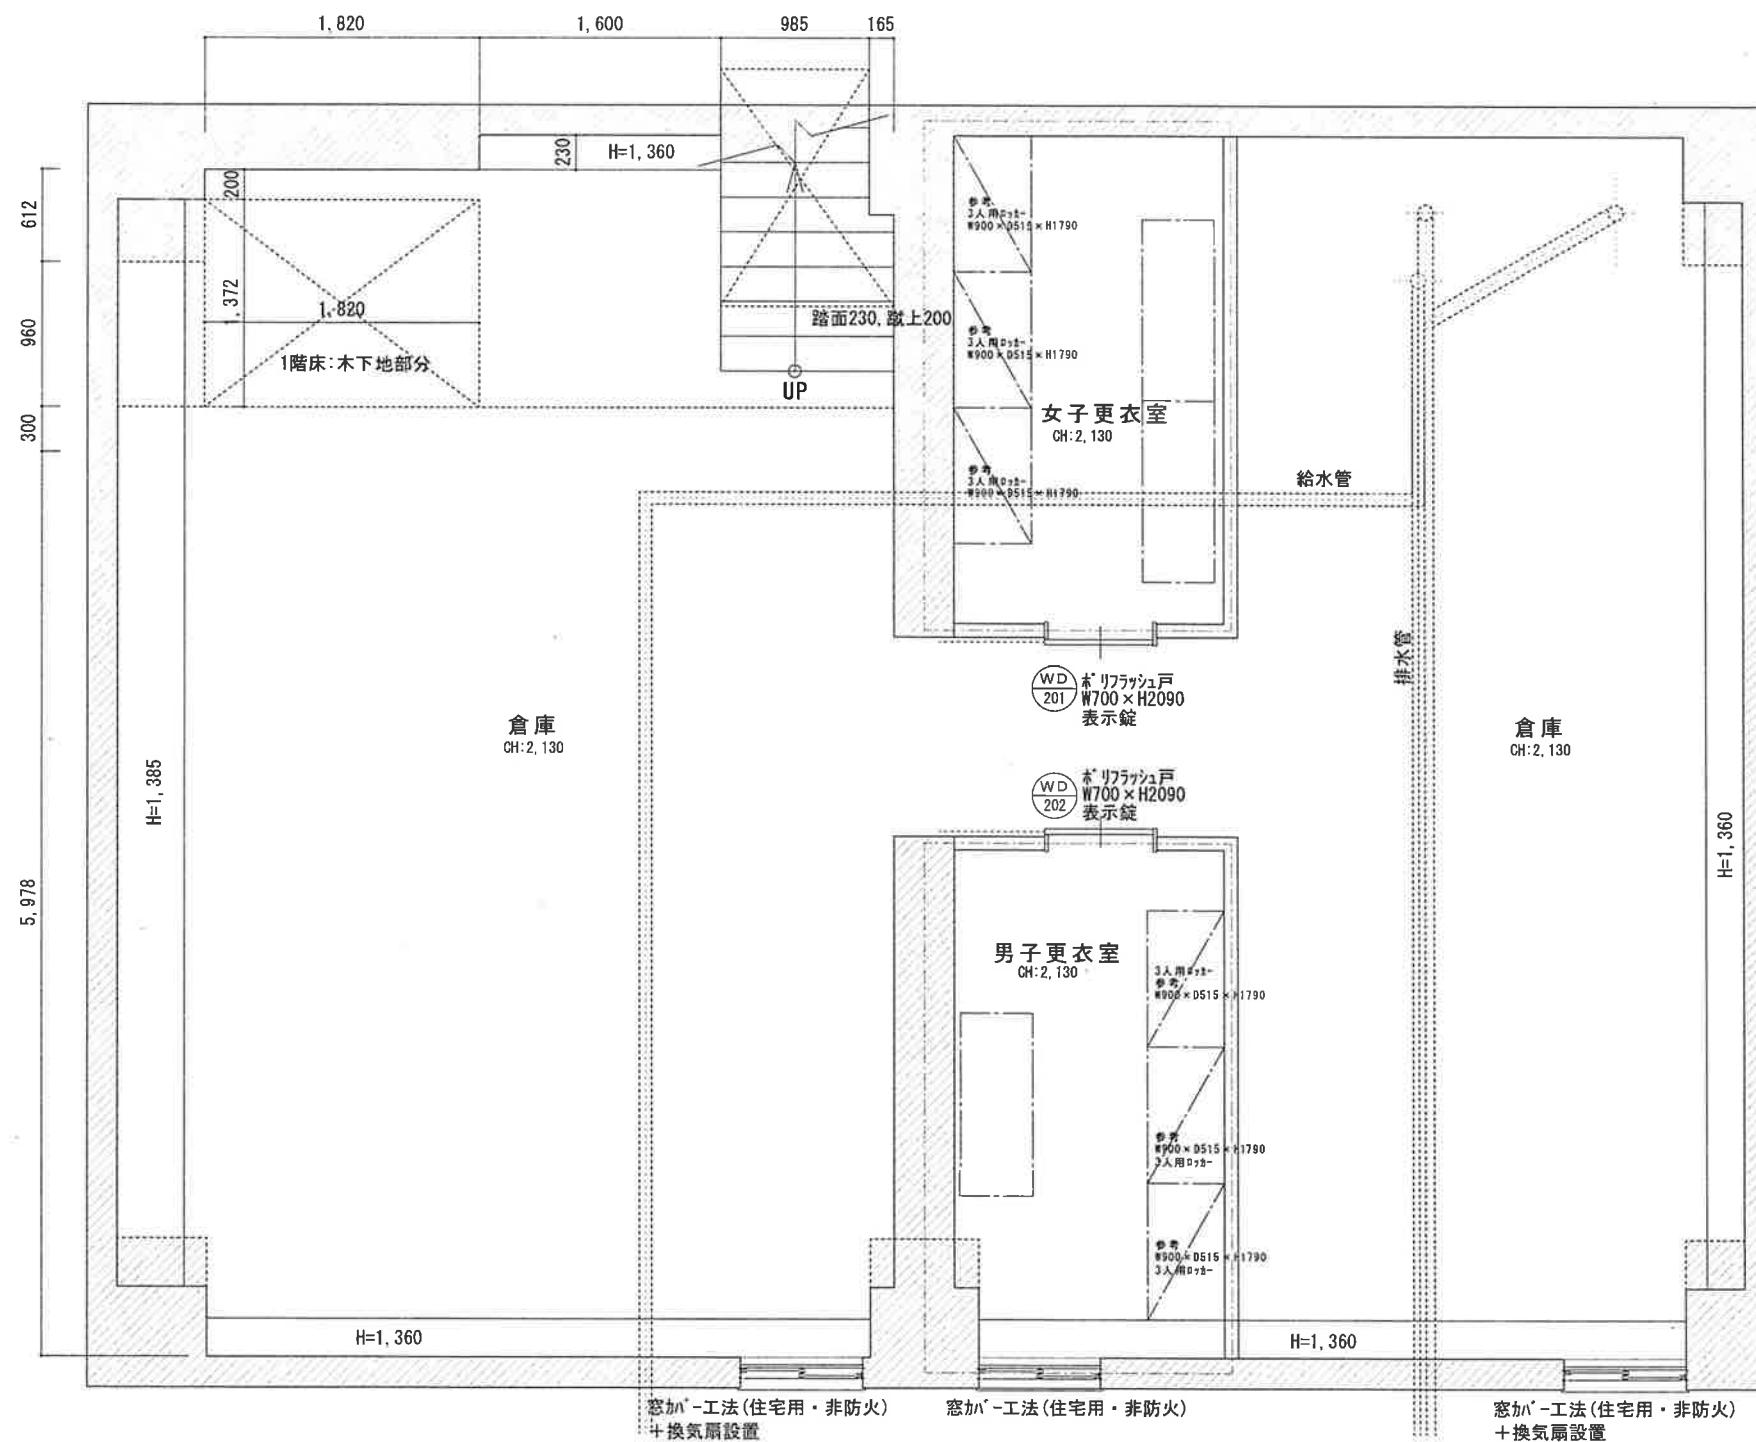


所在地：名古屋市西区名駅2-4-3


23.11.21
23.09.07
23.08.02
23.07.14

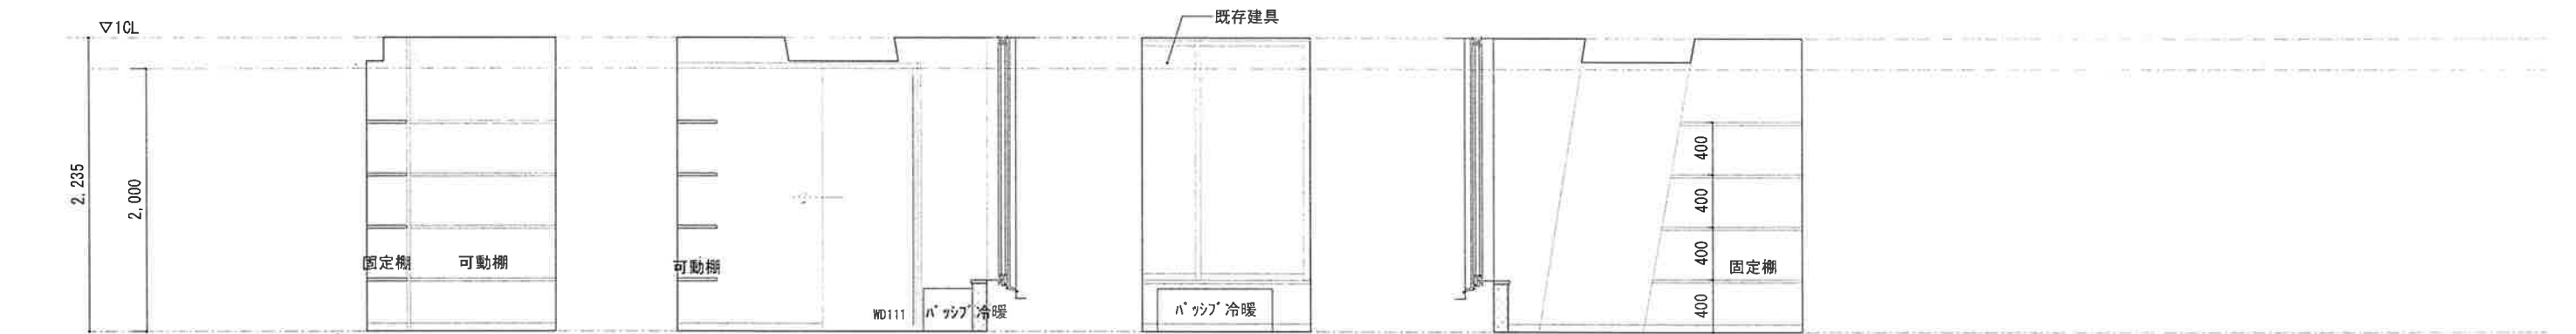

倉庫1 ー北ー ー東ー ー南ー ー西ー



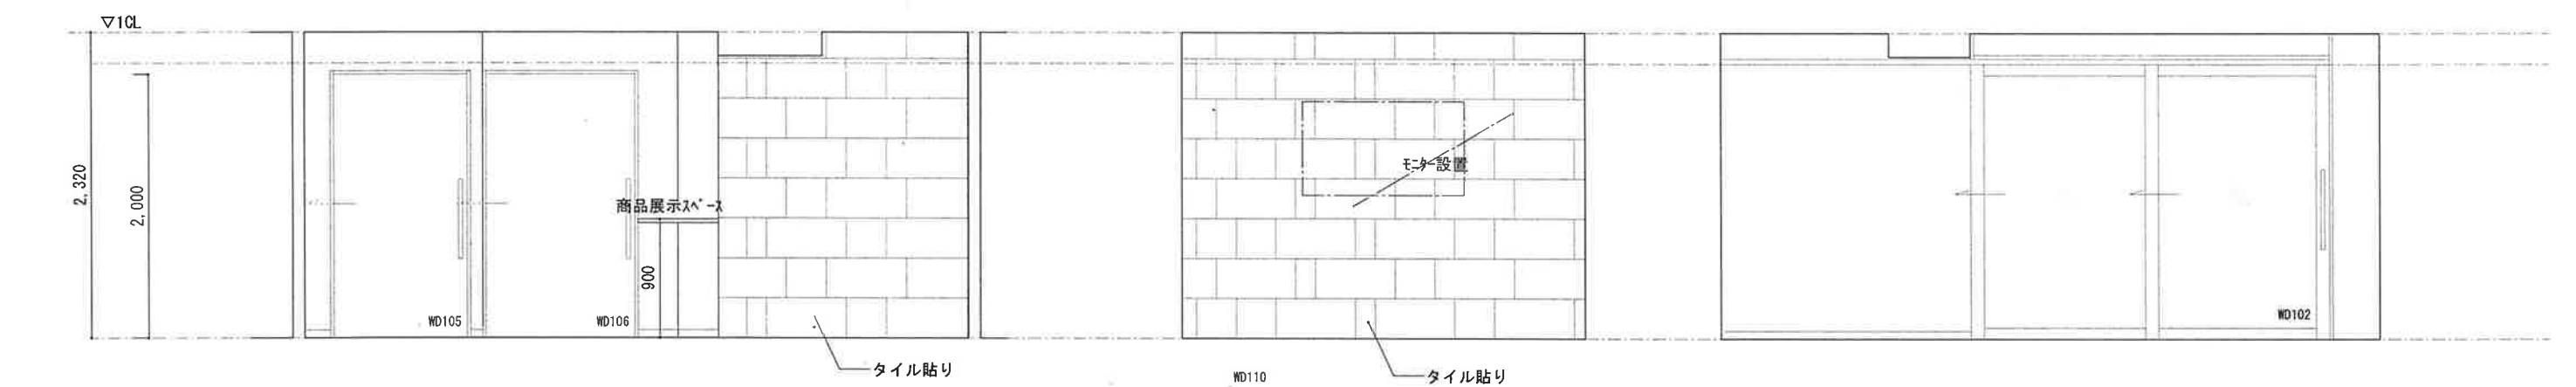





大会議室 ー北ー ー東ー ー南ー

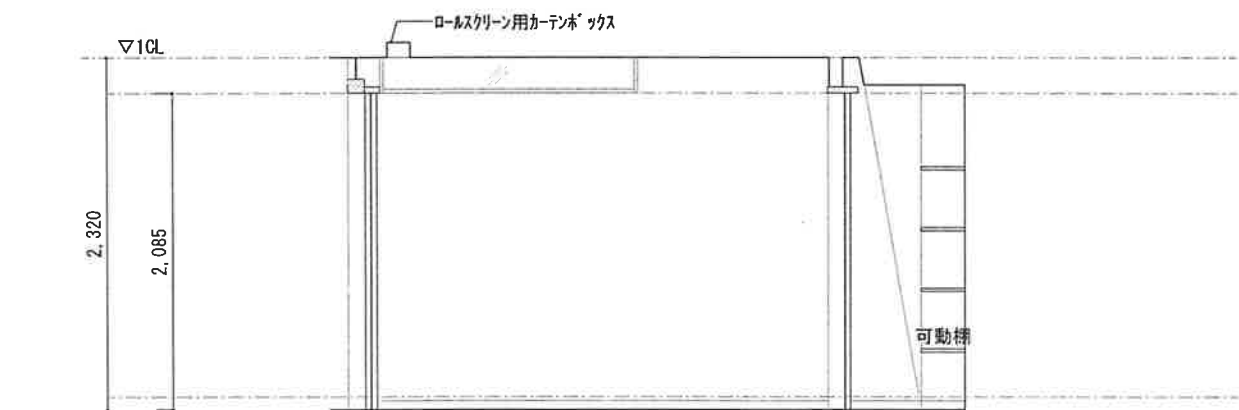




大会議室 ー西ー


24.01.31
23.11.17
23.11.15
23.11.14
23.10.05

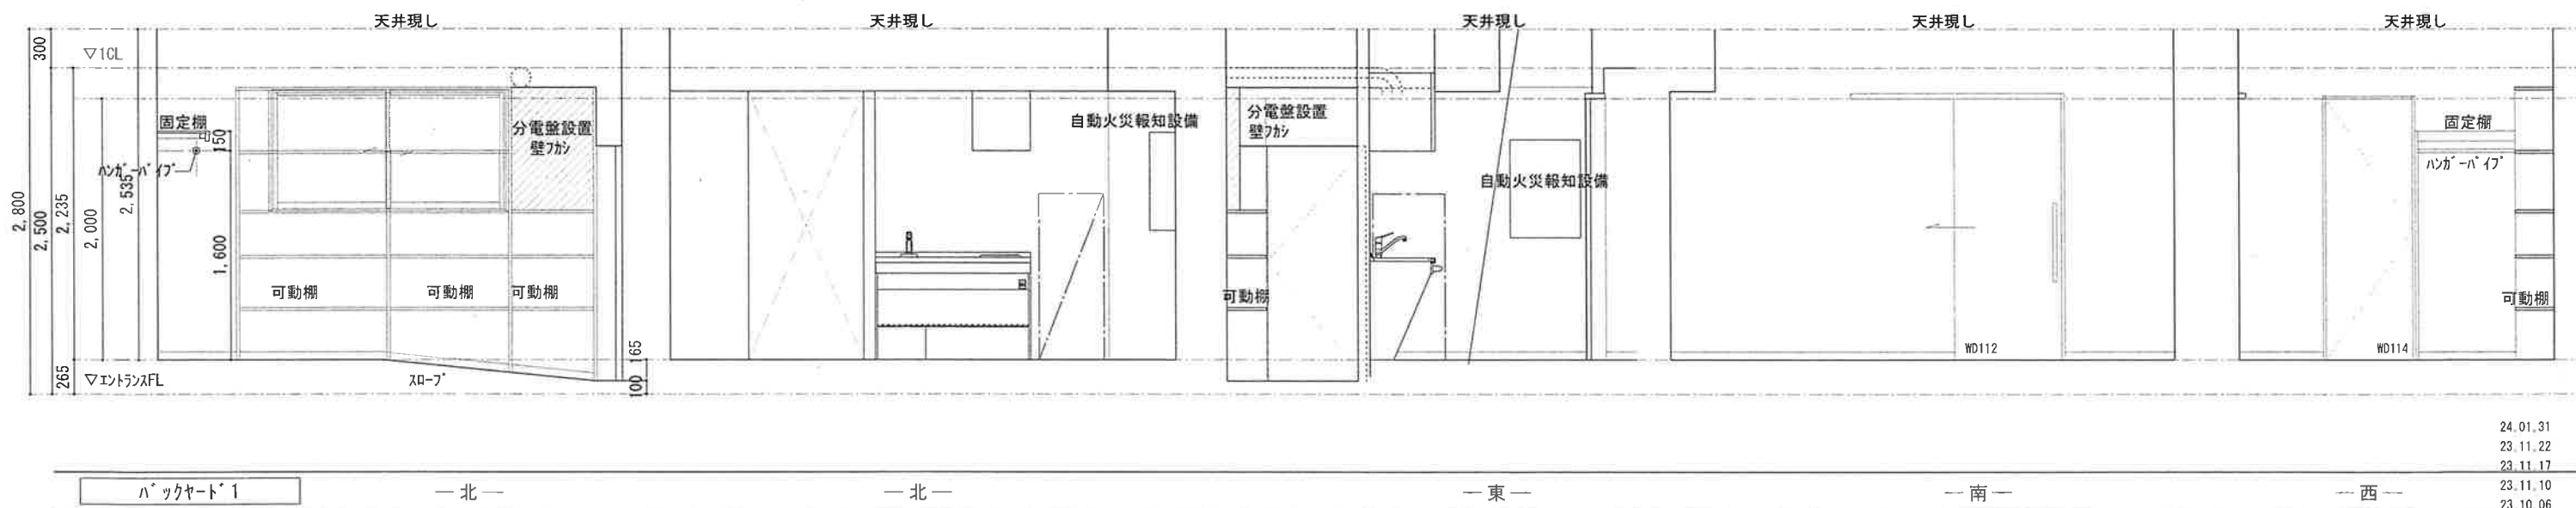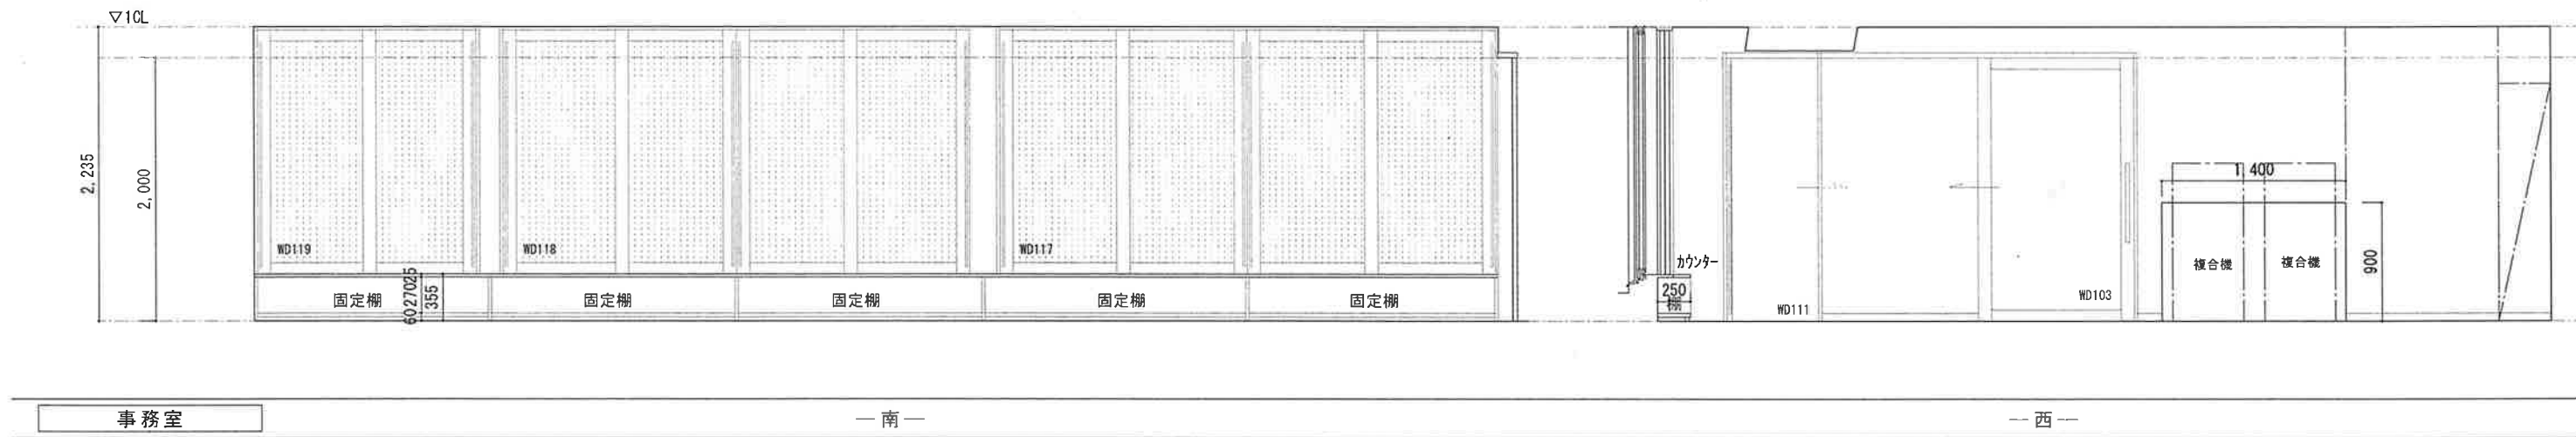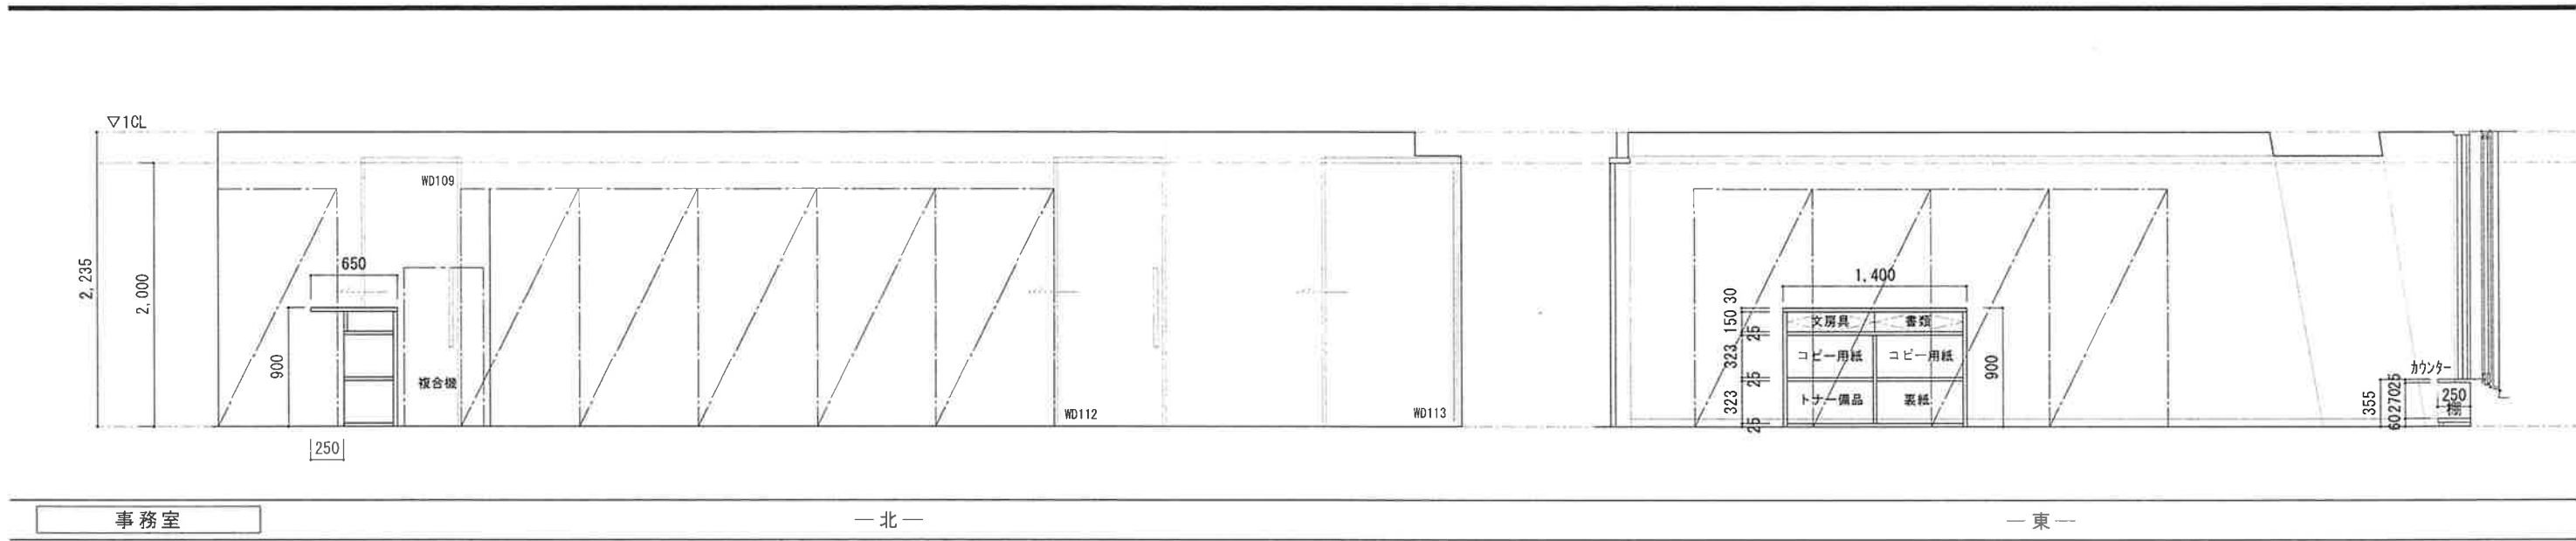

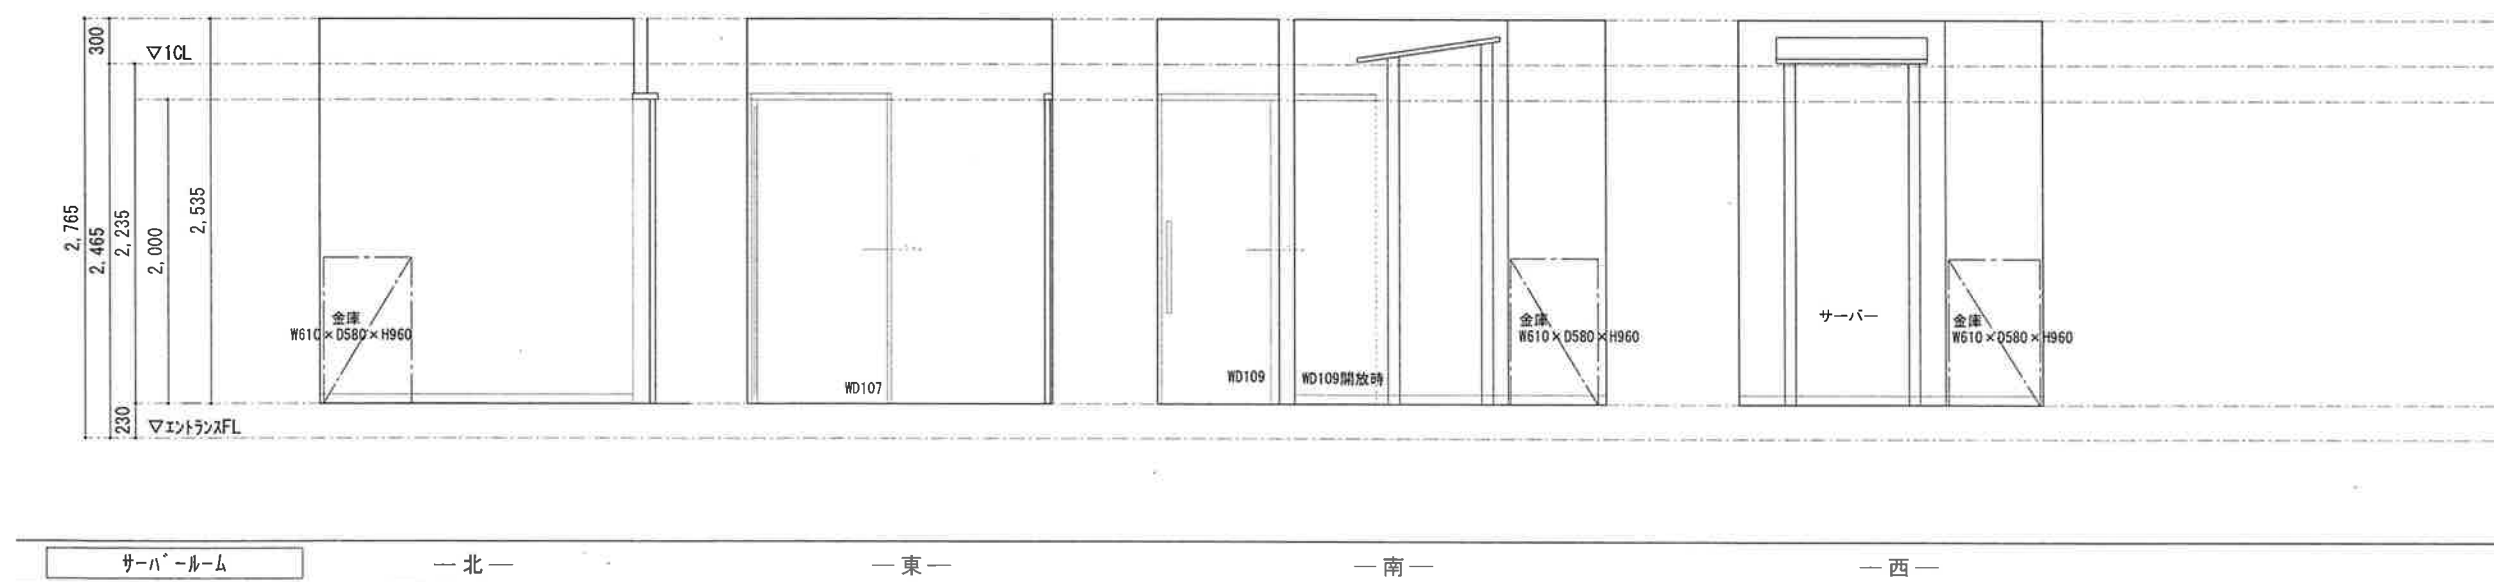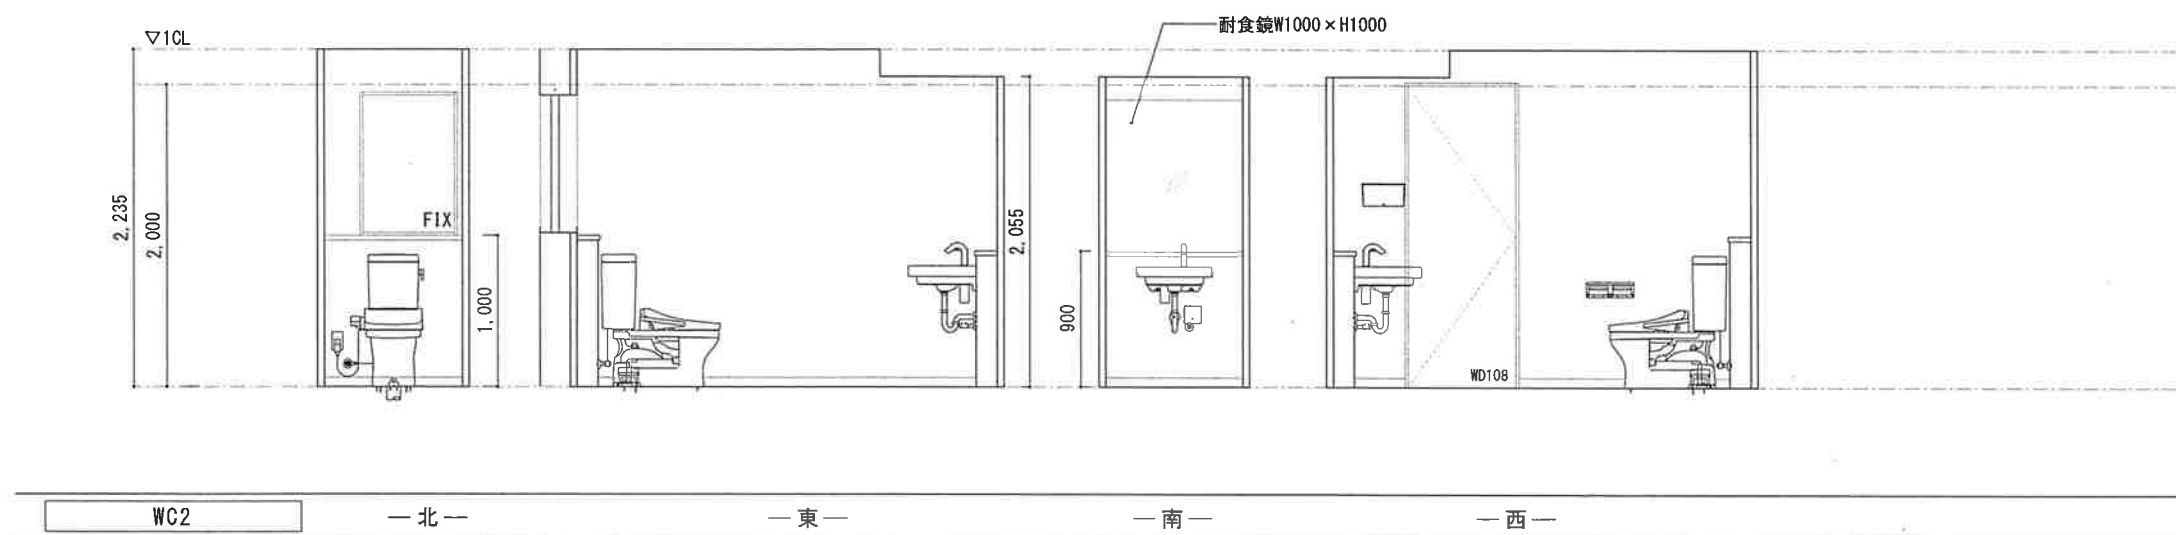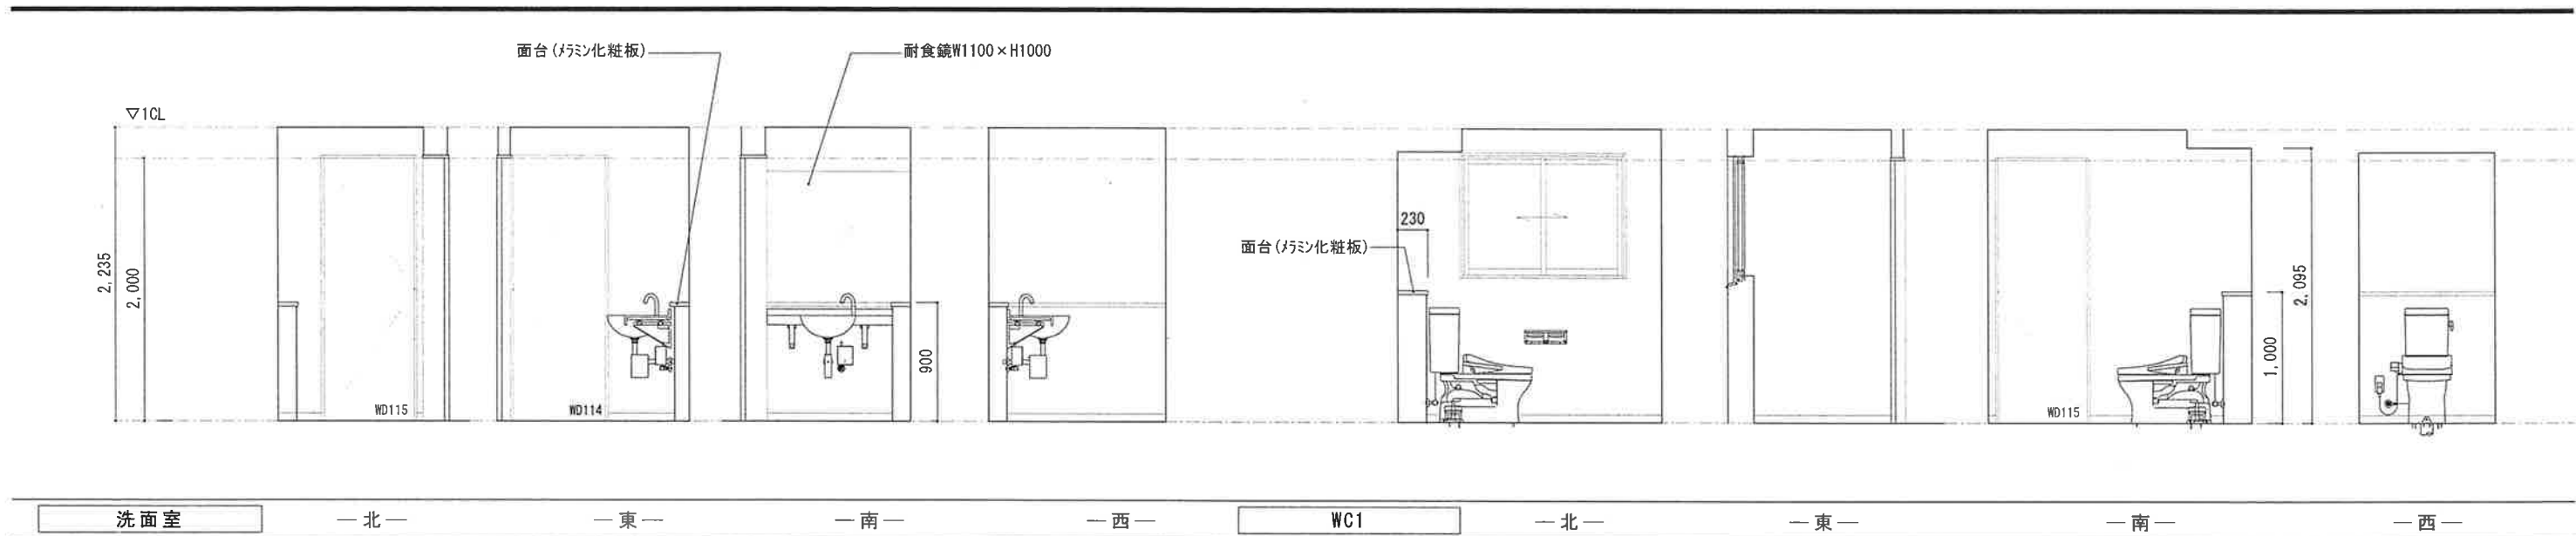


24.01.31
23.11.22
23.11.17
23.11.13
23.11.10
23.10.12

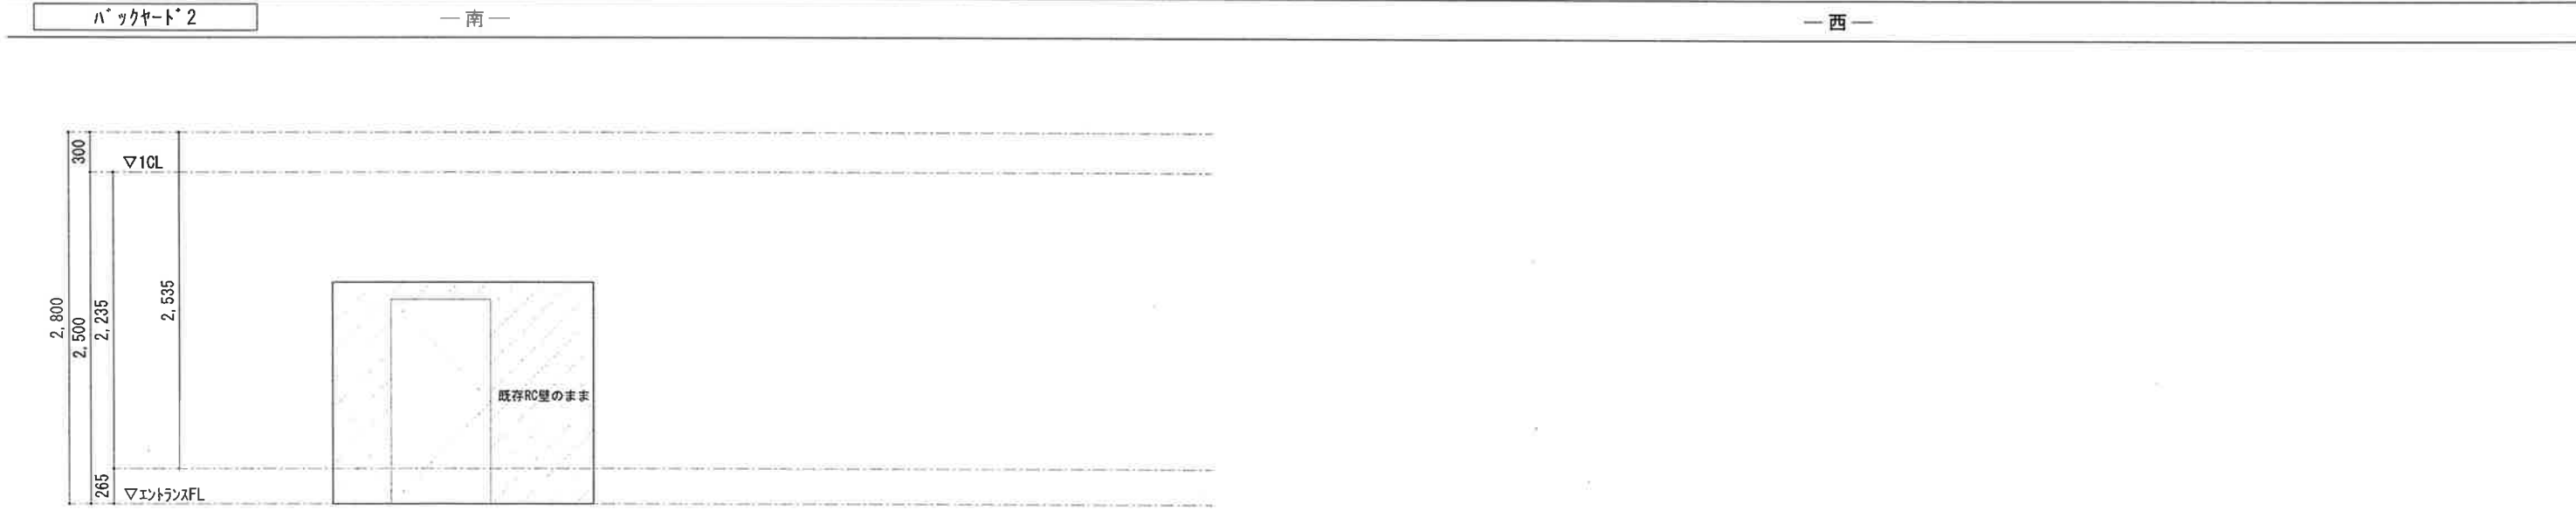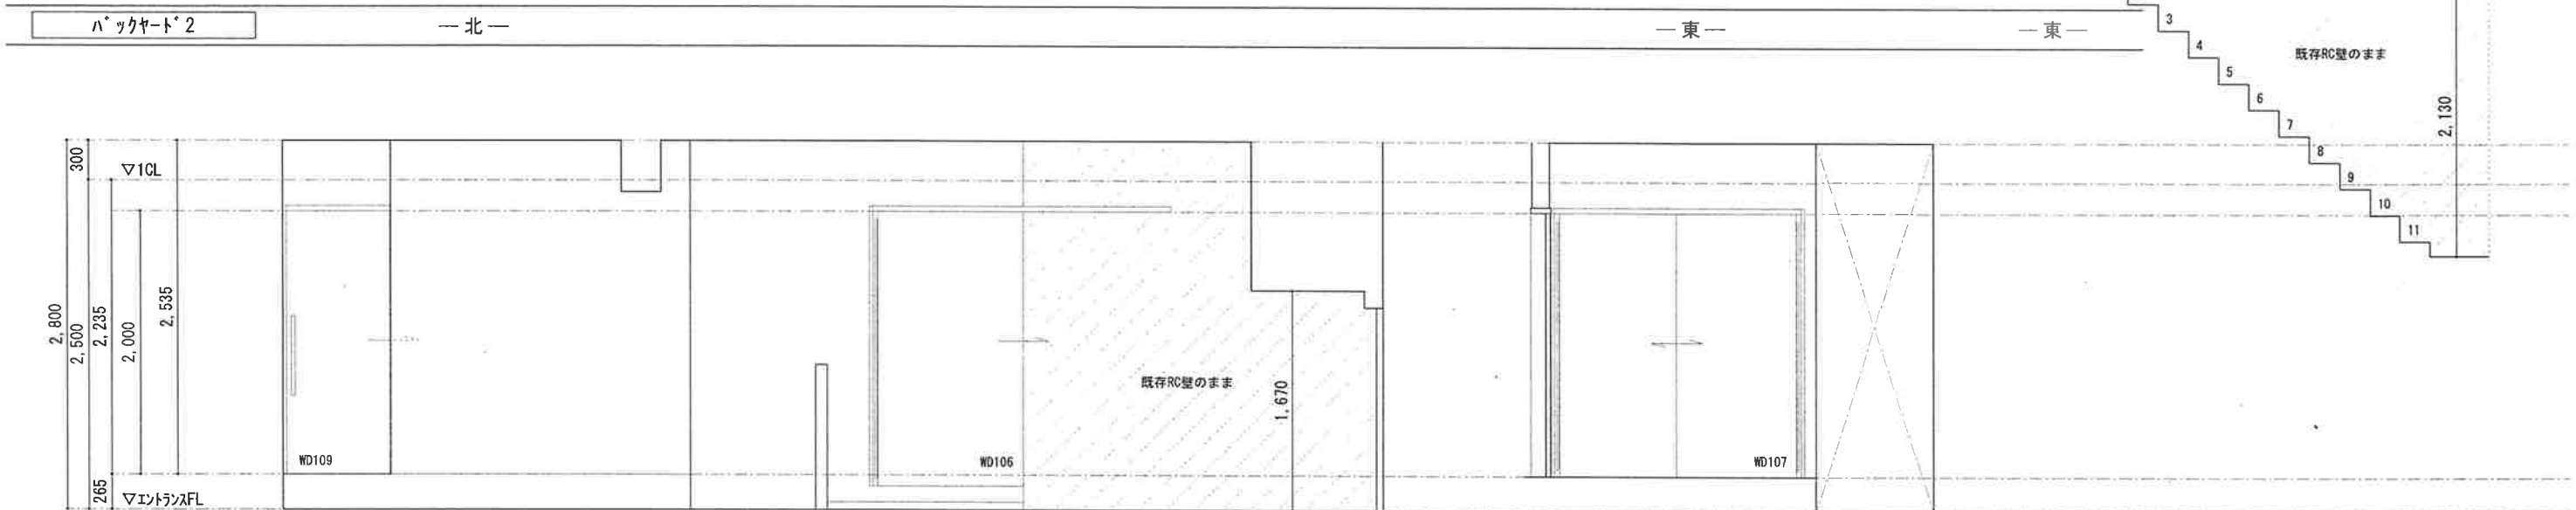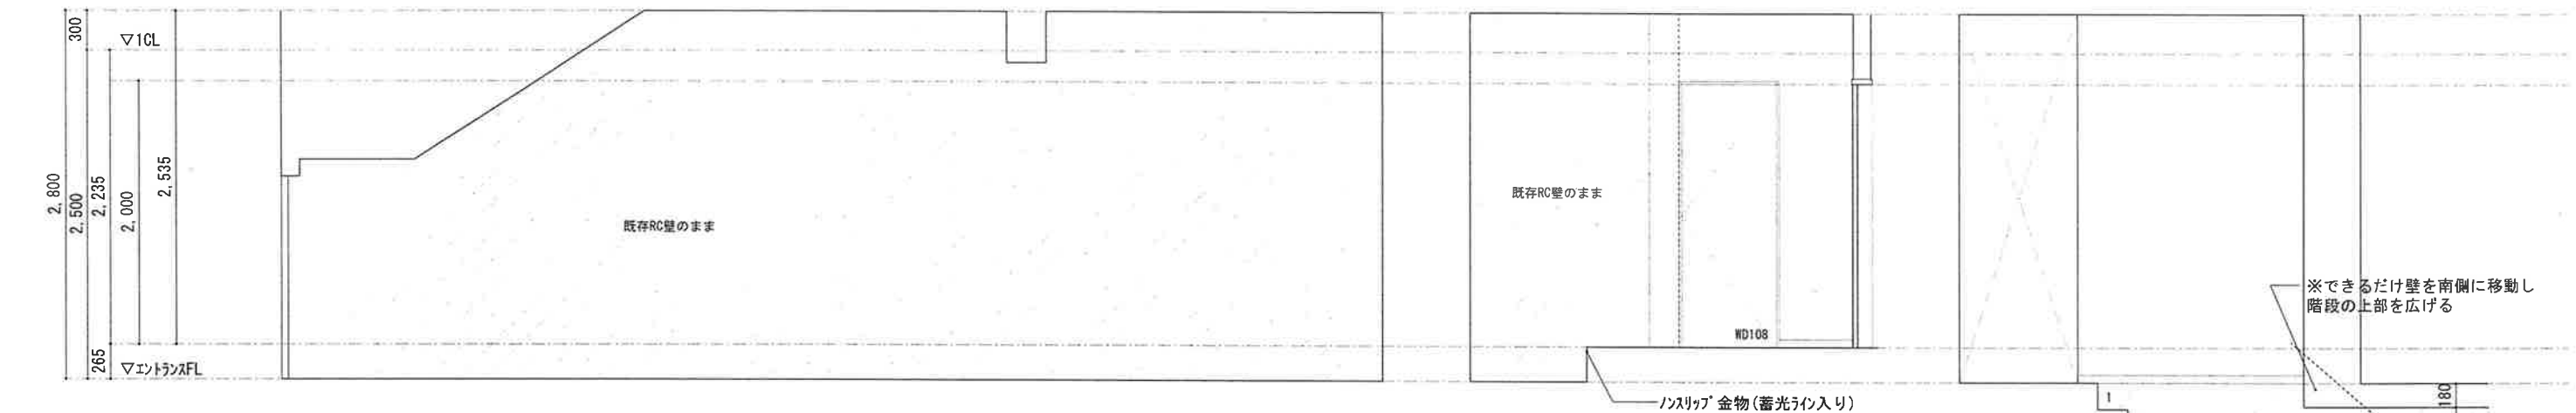








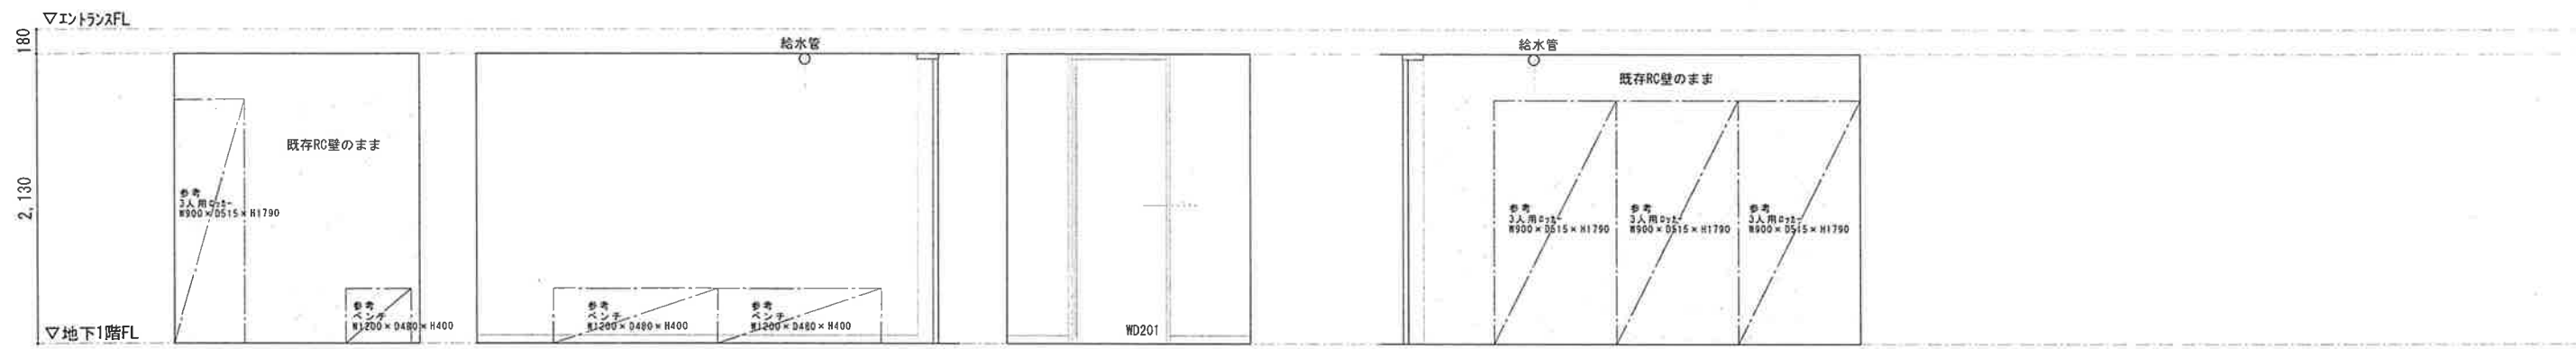








女子更衣室 — 北 — — 東 — — 南 — — 西 —

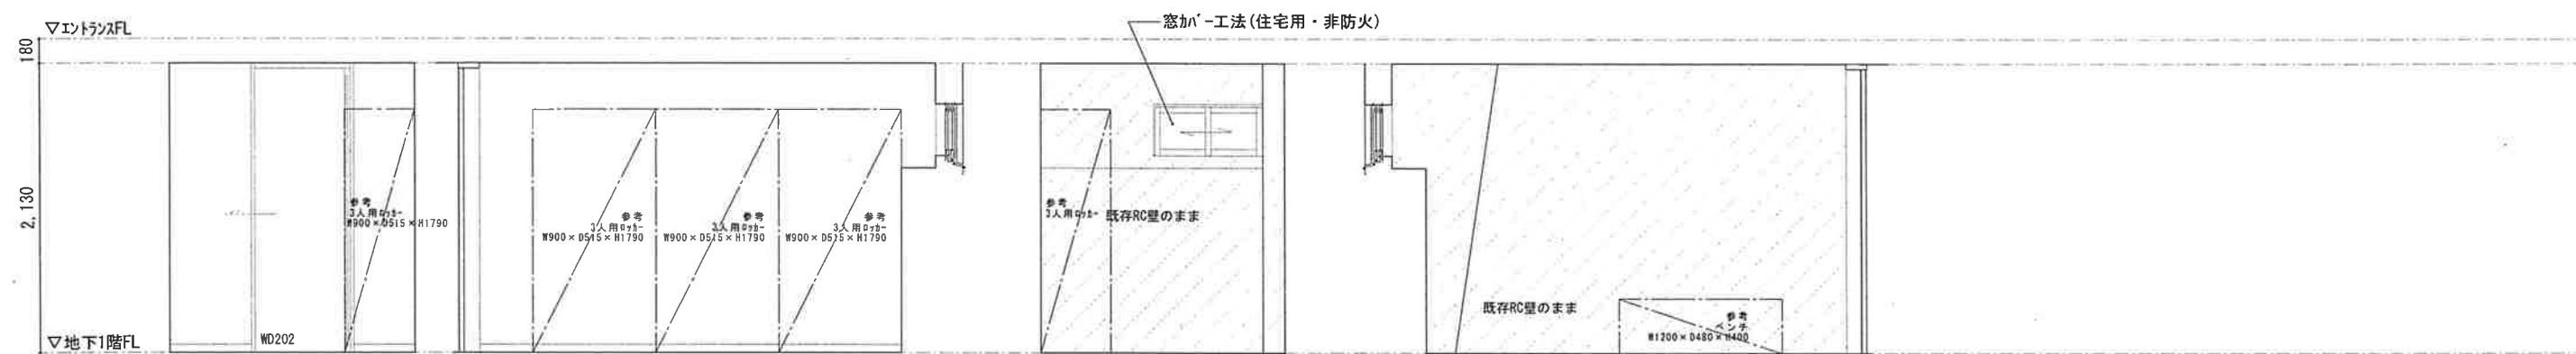


男子更衣室 — 北 — — 東 — — 南 — — 西 —

符 号	WD 101 吊 1 階 応接室兼会長室	WD 102 吊 1 階 大会議室	WD 103 吊 1 階 事務室	WD 104 1 階 大会議室
形状・寸法				
型式/建具厚	2枚連動片引き框戸 / 厚33	2枚連動片引き框戸 / 厚33	片引き框戸 / 厚33	両開きフラッシュ戸 / 厚33
材質/仕上	スプルス/ CL	スプルス/ CL	スプルス/ CL	ポリ合板 / CL 大手:スプルス
ガラス	強化ガラス 厚5	強化ガラス 厚5	強化ガラス 厚5	
金物 その他	吊レール: AFD-1300H シルバー クローザー付吊車(戸先): FC-2900-K-H 白 吊車(戸尻): AFD-2900-K 白 ×1コ 下ガイド: FG-051 引手: BEST/G974 L=400	吊レール: AFD-1300H シルバー クローザー付吊車(戸先): FC-2900-K-H 白 吊車(戸尻): AFD-2900-K 白 ×1コ 下ガイド: FG-051 引手: BEST/G974 L=400	吊レール: AFD-1300H シルバー クローザー付吊車(戸先): FC-2900-K-H 白 吊車(戸尻): AFD-2900-K 白 ×1コ 下ガイド: FG-051 引手: BEST/G974 L=400	丁番: スガツネ スライド丁番 H230 C26/26T 取手
備考	ソフトクローズ	ソフトクローズ	ソフトクローズ	
符 号	WD 105 吊 1 階 大会議室	WD 106 吊 1 階 大会議室	WD 107 吊 1 階 サーバルーム	
形状・寸法				
型式/建具厚	片引きフラッシュ戸 / 厚33	片引きフラッシュ戸 / 厚33	片引きフラッシュ戸 / 厚33	
材質/仕上	ポリ合板 / CL 大手:スプルス	ポリ合板 / CL 大手:スプルス	ポリ合板+手掛タモ/ CL 大手:スプルス	
ガラス				
金物 その他	吊レール: AFD-1300H シルバー クローザー付吊車(戸先): FC-2900-K-H 白 吊車(戸尻): AFD-2900-K 白 ×1コ 下ガイド: FG-051 引手: BEST/G974 L=400	吊レール: AFD-1300H シルバー クローザー付吊車(戸先): FC-2900-K-H 白 吊車(戸尻): AFD-2900-K 白 ×1コ 下ガイド: FG-051 引手: BEST/G974 L=400	吊レール: AFD-1300H シルバー クローザー付吊車(戸先): FC-2900-K-H 白 吊車(戸尻): AFD-2900-K 白 ×1コ 下ガイド: FG-051 引手: タモ材掘り込み 鍵: シンダー錠	
備考	ソフトクローズ	ソフトクローズ	ソフトクローズ	

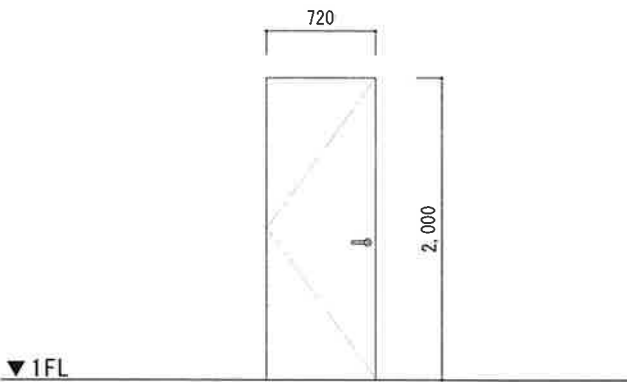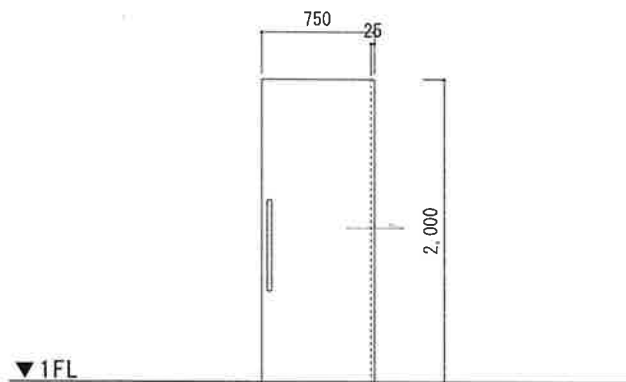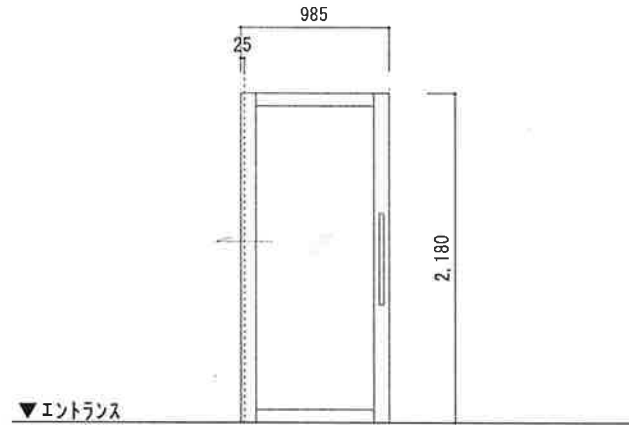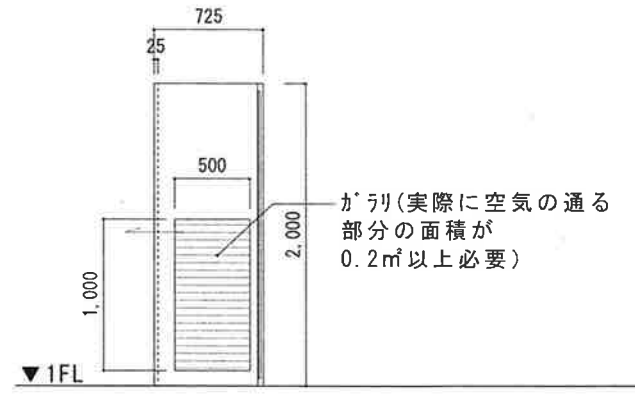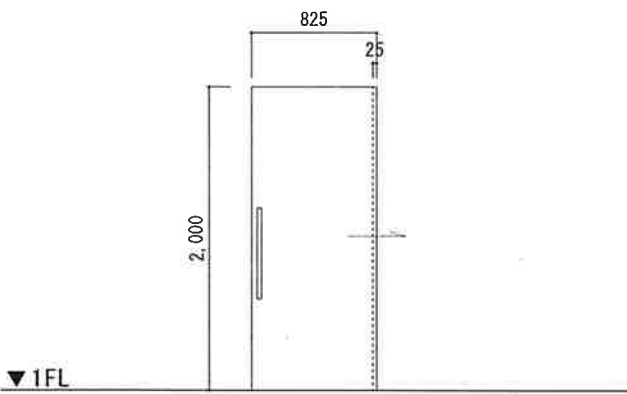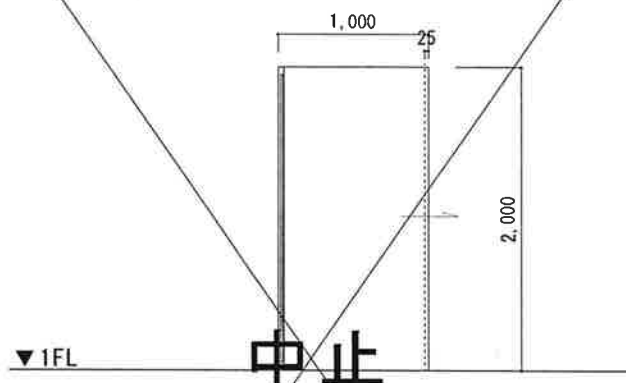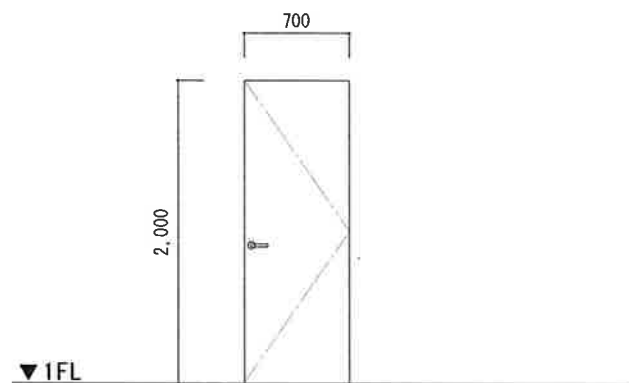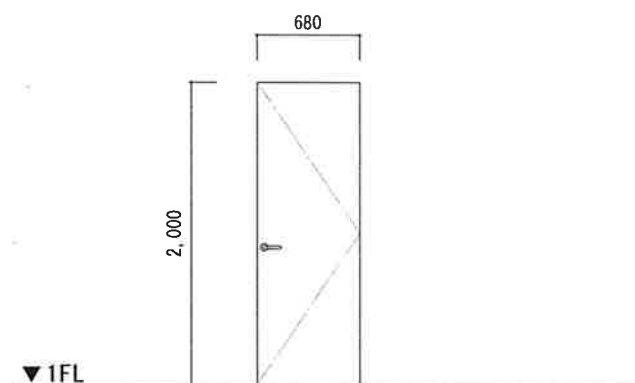
符 号	WD 108	1 階 WC2	WD 109	吊	1 階 事務所	WD 110	吊	1 階 エントランス	WD 111	吊	1 階 倉庫 1
形状・寸法											
型式/建具厚	片開きフラッシュ戸 / 厚33		片引きフラッシュ戸 / 厚33		片引き框戸 / 厚33		片引きフラッシュ戸 / 厚33				
材質/仕上	ポリ合板 / CL 大手: スプルス		ポリ合板+手掛タモ/ CL 大手: スプルス		スプルス/ CL		ポリ合板+手掛タモ/ CL 大手: スプルス				
ガラス					強化ガラス 厚5						
金 物 その他	丁番: スガツネ スライド丁番 H230 C26/26T レバーハンドル 鍵: 表示錠		吊レール: AFD-1300H シルバー クローザー付吊車(戸先): FC-2900-K-H 白 吊車(戸尻): AFD-2900-K 白 ×1コ 下ガイド: FG-051 引 手: BEST/G974 L=400		吊レール: AFD-1300H シルバー クローザー付吊車(戸先): FC-2900-K-H 白 吊車(戸尻): AFD-2900-K 白 ×1コ 下ガイド: FG-051 引 手: タモ材掘り込み		吊レール: AFD-1300H シルバー クローザー付吊車(戸先): FC-2900-K-H 白 吊車(戸尻): AFD-2900-K 白 ×1コ 下ガイド: FG-051 引 手: タモ材掘り込み				
備 考			ソフトクローズ		ソフトクローズ		ソフトクローズ				
符 号	WD 112	吊	WD 113	吊	WD 114	1 階 洗面室	WD 115	1 階 WC1			
形状・寸法											
型式/建具厚	片引きフラッシュ戸 / 厚33		片引きフラッシュ戸 / 厚33		片開きフラッシュ戸 / 厚33		片開きフラッシュ戸 / 厚33				
材質/仕上	ポリ合板+手掛タモ/ CL 大手: スプルス		ポリ合板+手掛タモ/ CL 大手: スプルス		ポリ合板 / CL 大手: スプルス		ポリ合板 / CL 大手: スプルス				
ガラス											
金 物 その他	吊レール: AFD-1300H シルバー クローザー付吊車(戸先): FC-2900-K-H 白 吊車(戸尻): AFD-2900-K 白 ×1コ 下ガイド: FG-051 引 手: BEST/G974 L=400		吊レール: AFD-1300H シルバー クローザー付吊車(戸先): FC-2900-K-H 白 吊車(戸尻): AFD-2900-K 白 ×1コ 下ガイド: FG-051 引 手: タモ材掘り込み		丁番: スガツネ スライド丁番 H230 C26/26T レバーハンドル		丁番: スガツネ スライド丁番 H230 C26/26T レバーハンドル 鍵: 表示錠				
備 考	ソフトクローズ		ソフトクローズ								

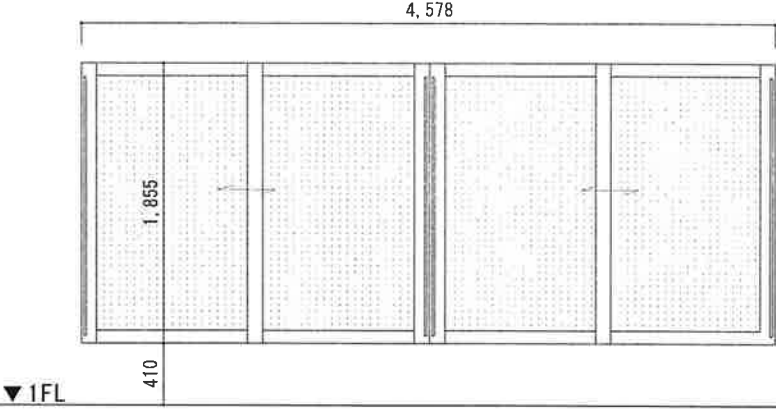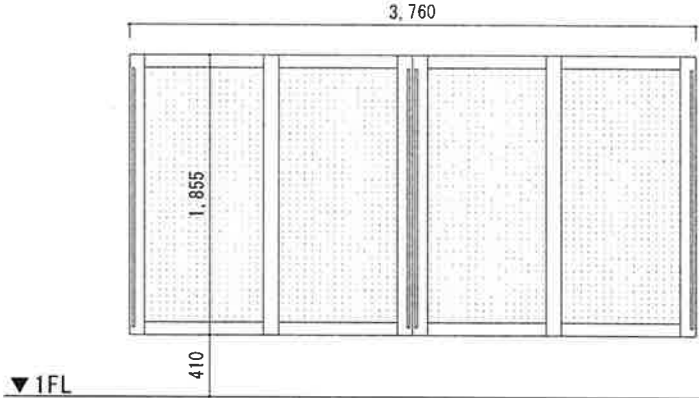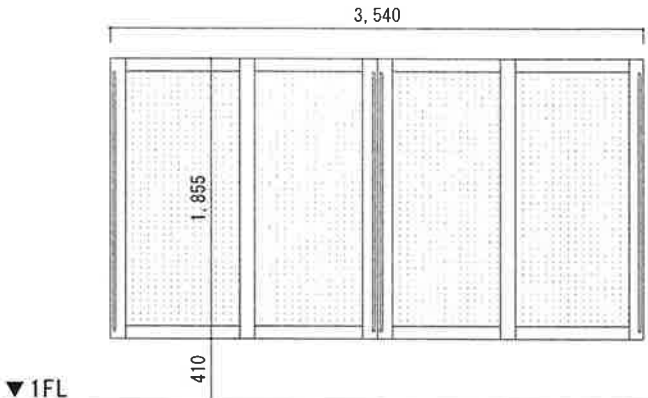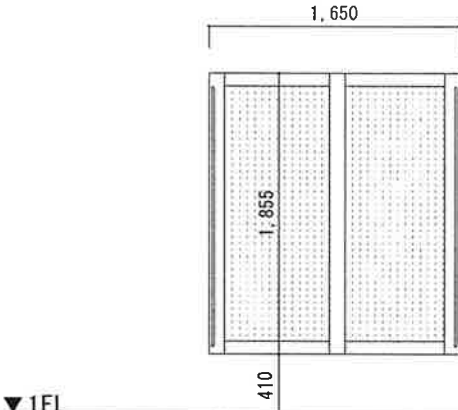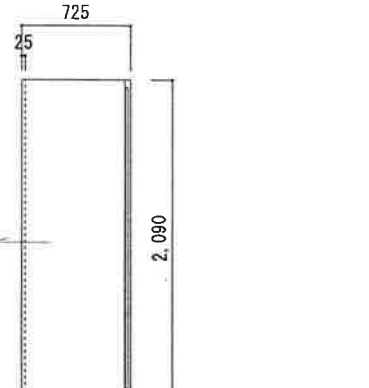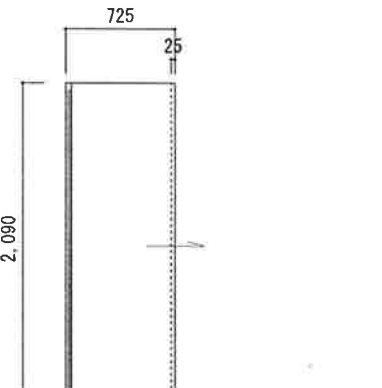符 号	WD 116 吊	1 階 応接室	WD 117 吊	1 階 事務所	WD 118 吊	1 階 事務所
形状・寸法						
型式/建具厚	4本引違い框戸 / 厚33		4本引違い框戸 / 厚33		4本引違い框戸 / 厚33	
材質/仕上	スプルス/ CL		スプルス/ CL		スプルス/ CL	
ガラス	ホリカツイン 乳白 厚6		ホリカツイン 乳白 厚6		ホリカツイン 乳白 厚6	
金物 その他	吊レール: AFD-1300H シルバー クローザー付吊車(戸先): FC-2900-K-H 白 吊車(戸尻): AFD-2900-K 白 × 1コ 下ガイド: FG-051 引手: 掘り込み		吊レール: AFD-1300H シルバー クローザー付吊車(戸先): FC-2900-K-H 白 吊車(戸尻): AFD-2900-K 白 × 1コ 下ガイド: FG-051 引手: 掘り込み		吊レール: AFD-1300H シルバー クローザー付吊車(戸先): FC-2900-K-H 白 吊車(戸尻): AFD-2900-K 白 × 1コ 下ガイド: FG-051 引手: 掘り込み	
備 考	ソフトクローズ					
符 号	WD 119 吊	1 階 事務所	WD 201 吊	地下 女子更衣室	WD 202 吊	地下 男子更衣室
形状・寸法						
型式/建具厚	引違い框戸 / 厚33		片引きフラッシュ戸 / 厚33		片引きフラッシュ戸 / 厚33	
材質/仕上	スプルス/ CL		ポリ合板+手掛タモ/ CL 大手: スプルス		ポリ合板+手掛タモ/ CL 大手: スプルス	
ガラス	ホリカツイン 乳白 厚6					
金物 その他	吊レール: AFD-1300H シルバー クローザー付吊車(戸先): FC-2900-K-H 白 吊車(戸尻): AFD-2900-K 白 × 1コ 下ガイド: FG-051 引手: 掘り込み		吊レール: AFD-1300H シルバー クローザー付吊車(戸先): FC-2900-K-H 白 吊車(戸尻): AFD-2900-K 白 × 1コ 下ガイド: FG-051 引手: タモ材掘り込み 鍵: 表示錠		吊レール: AFD-1300H シルバー クローザー付吊車(戸先): FC-2900-K-H 白 吊車(戸尻): AFD-2900-K 白 × 1コ 下ガイド: FG-051 引手: タモ材掘り込み 鍵: 表示錠	
備 考		ソフトクローズ		ソフトクローズ		

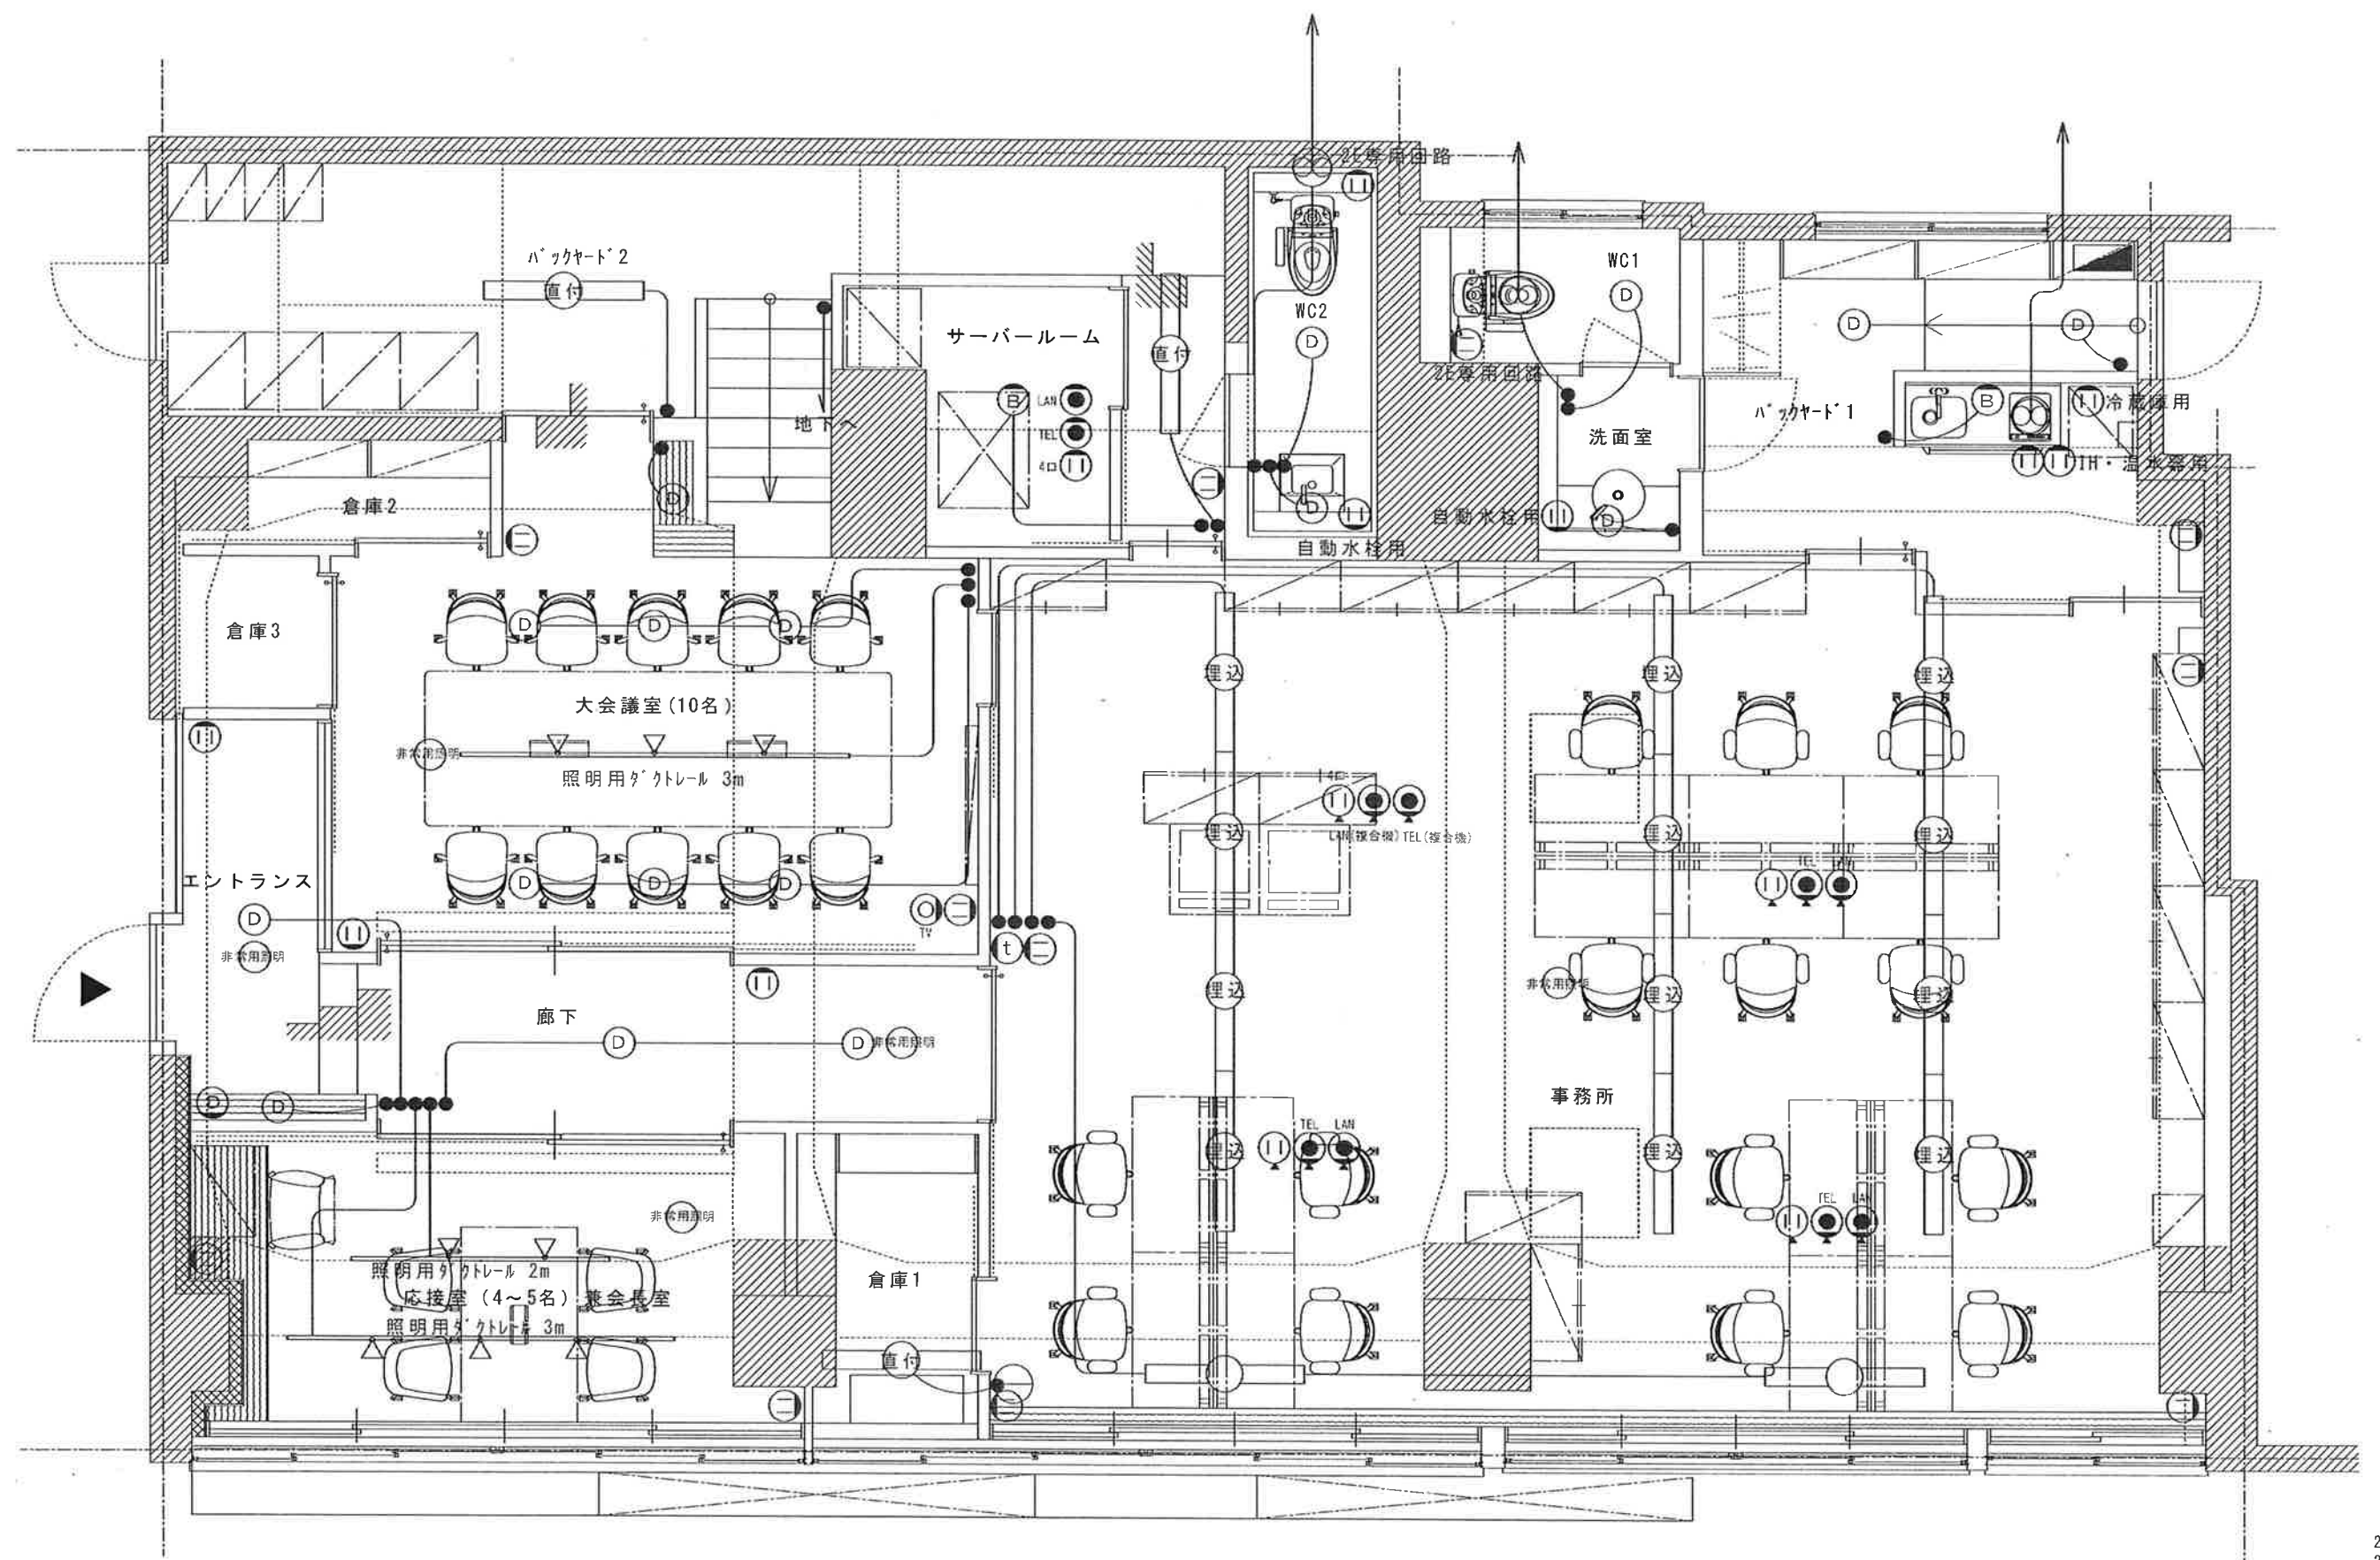

23.11.24
23.11.15
23.11.10
23.10.16
23.07.25

所在地：名古屋市西区名駅2-4-3

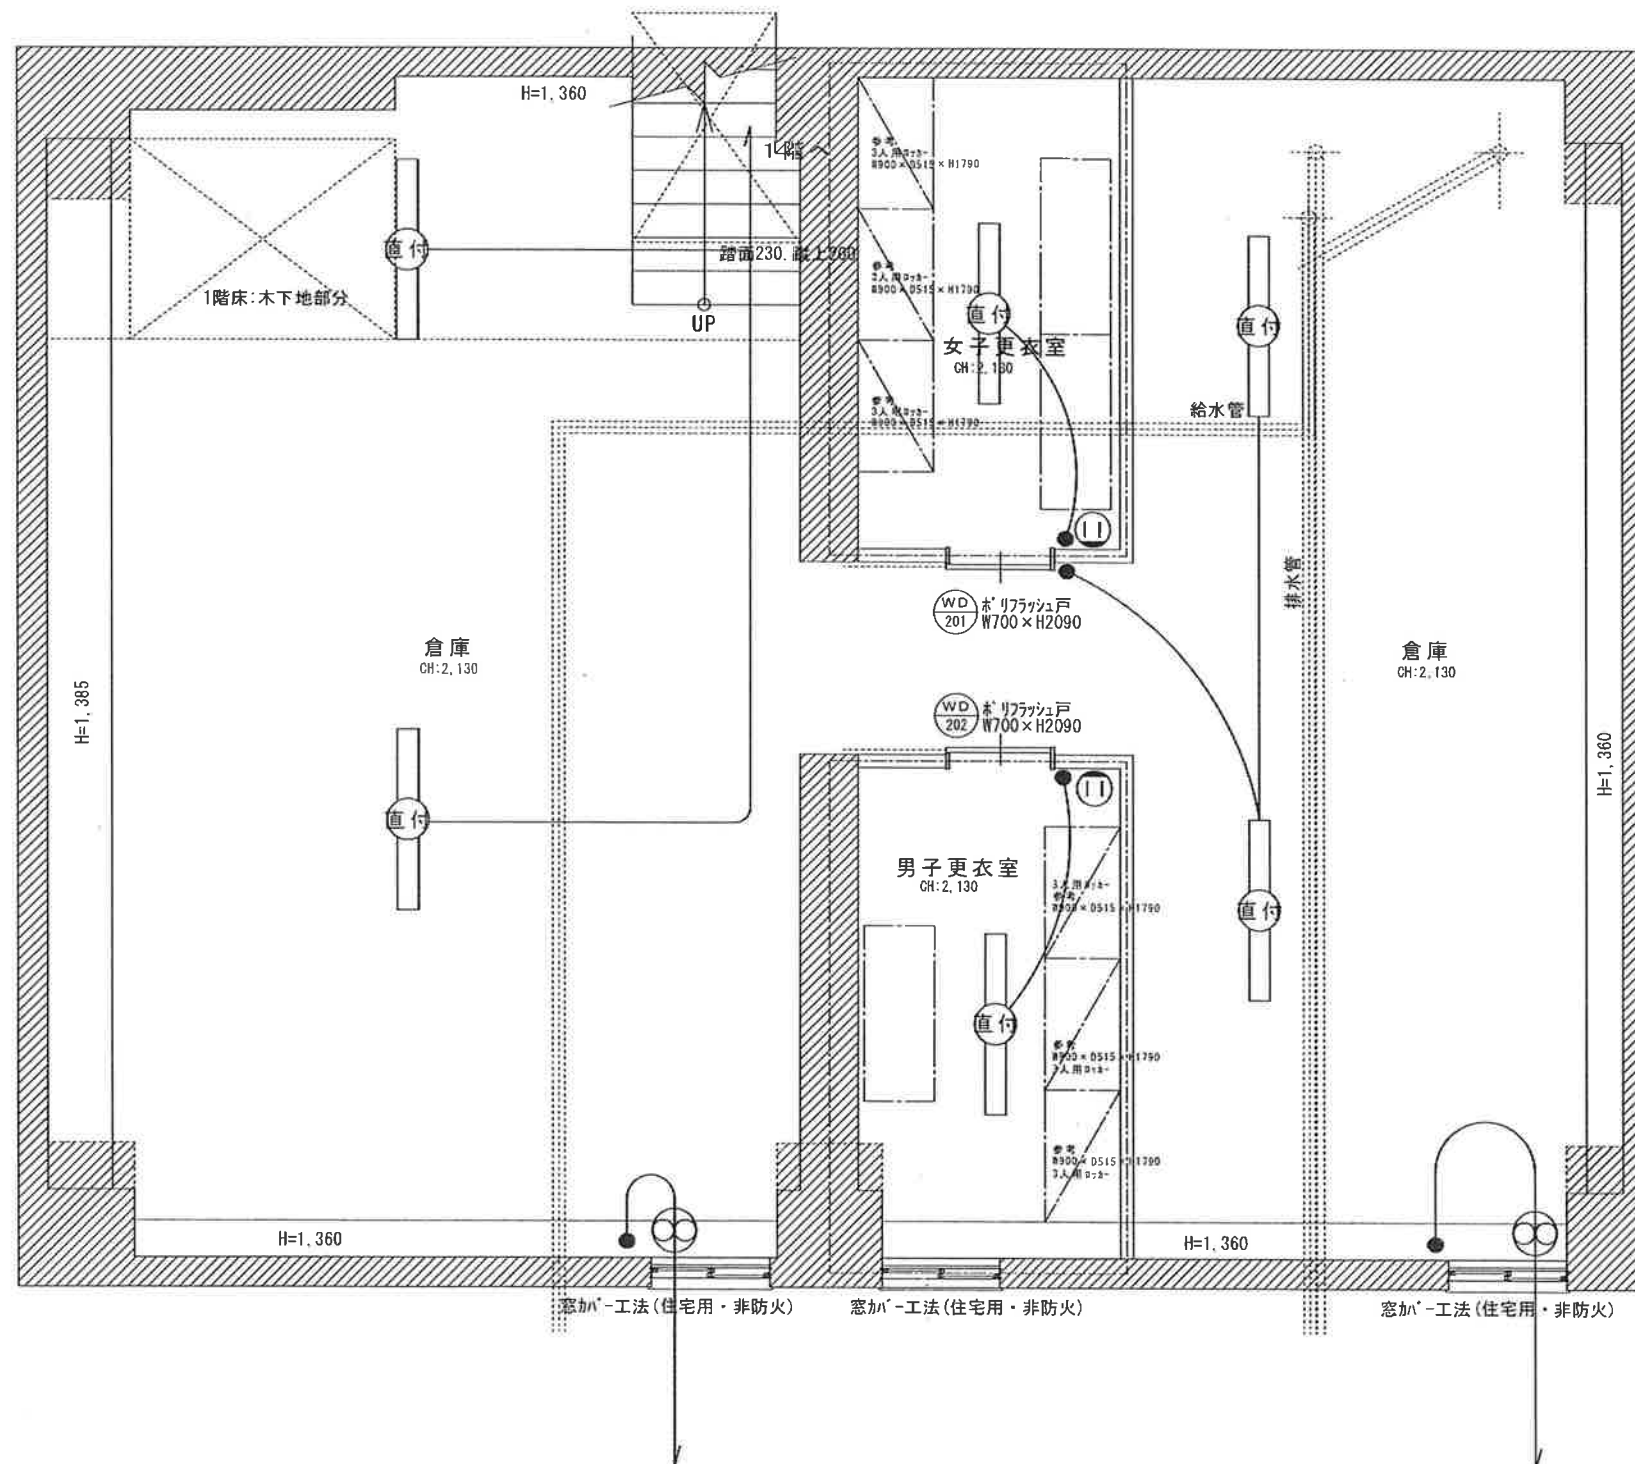

所在地：名古屋市西区名駅2-4-3

誠実建築

～阿部建設の家～

工事名

名古屋製綱本社 改修工事

図面名

地階電気設備図 S=1/50


木の香り設計工房

一級建築士登録第350723号
中村 徹

23.11.24
23.11.15
23.10.16
23.07.26

NO. E-2

名古屋製綱本社 改修工事 (1)

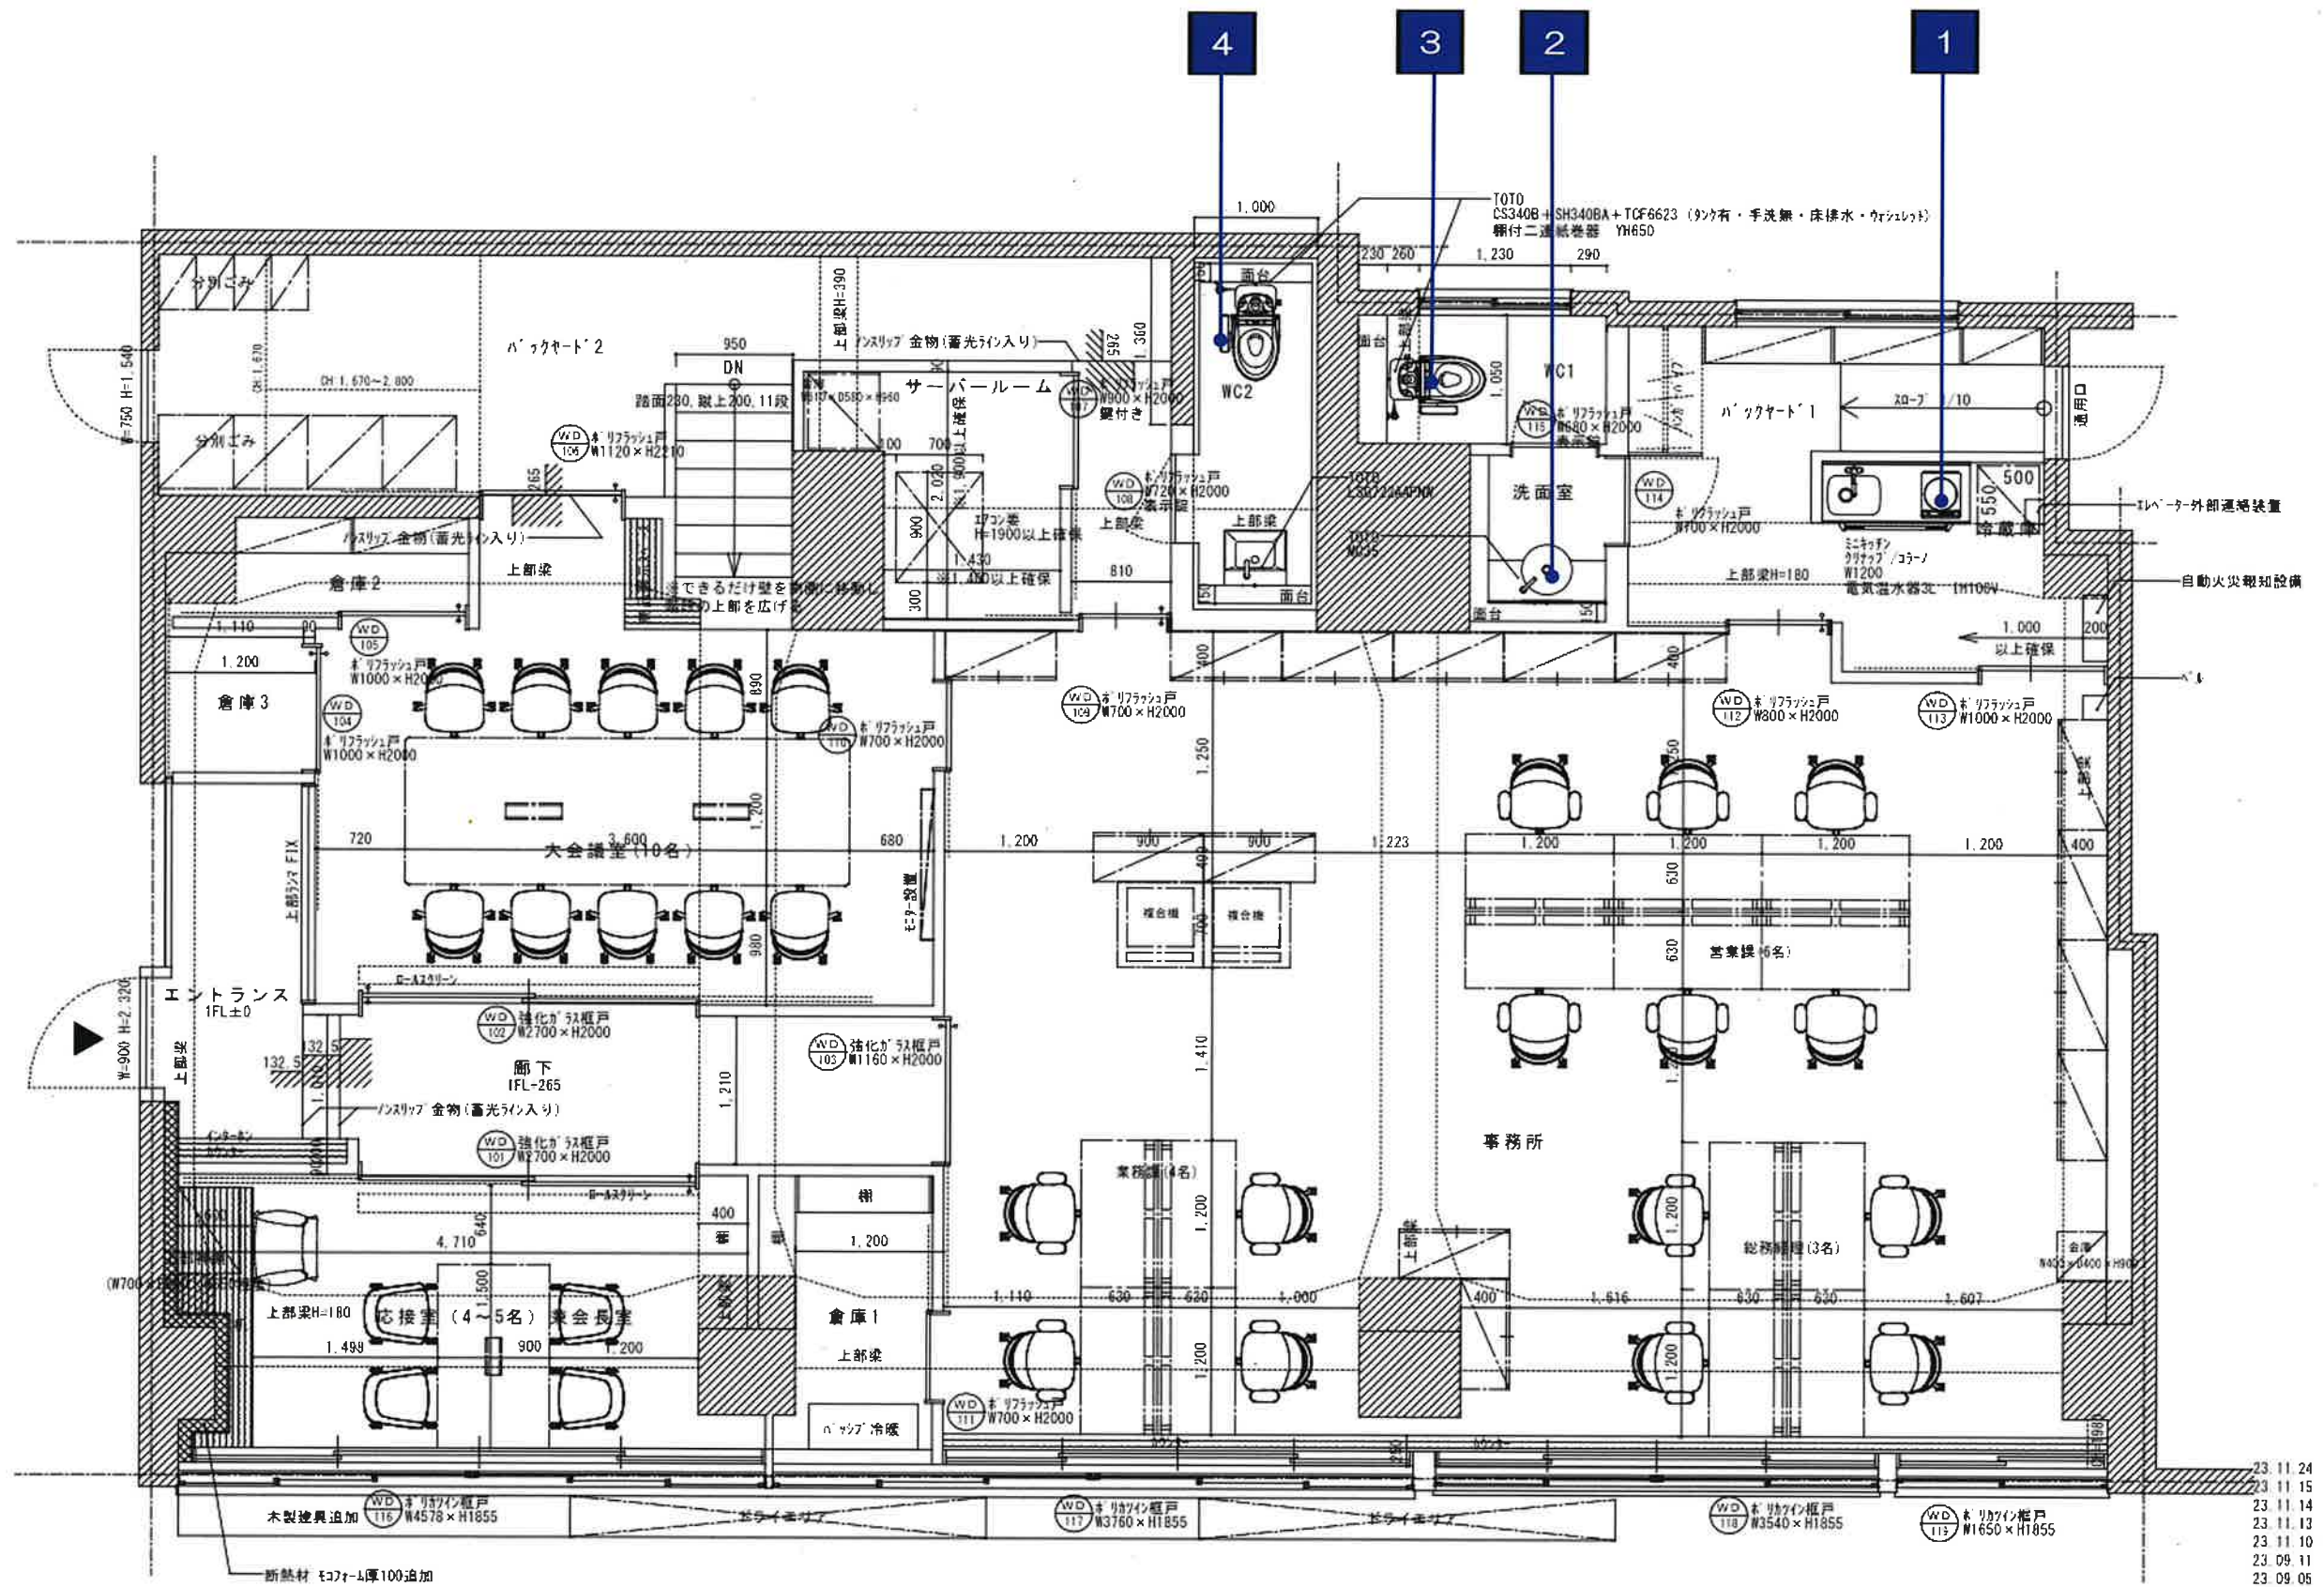

< 1階平面図 >

1

バックヤード1



イメージ写真

クリナップ/コラーノ セパレートタイプ
W1200(ホワイト)
ワークトップ/ステンレス
IHクッキングヒーター100V



イメージ写真

クリナップ/コラーノ レンジフード
W450
ZZWXS4550SW-F

2

洗面室



イメージ写真

MC35+TLE28SS1A
洗面器+自動水栓
(水石けん入れ無し・
自動水栓(温水器無し)・



YKT100R
ペーパータオルホルダー



MMA6A1000A1200W
フリーサイズ大型鏡

3

WC1



CS340B+SH340BA
腰掛式便器+ロータンク



TCF6623
ウォシュレットSB



YH702
棚付二連紙巻器

4

WC2



CS340B+SH340BA
腰掛式便器+ロータンク



TCF6623
ウォシュレットSB



YH702
棚付二連紙巻器



YKT100R
ペーパータオルホルダー



イメージ写真
LSG722AAPNW
壁掛洗面器
(水石けん入れ無し・
自動水栓(温水器無し)・



MMA6A1000A1000W
フリーサイズ大型鏡